
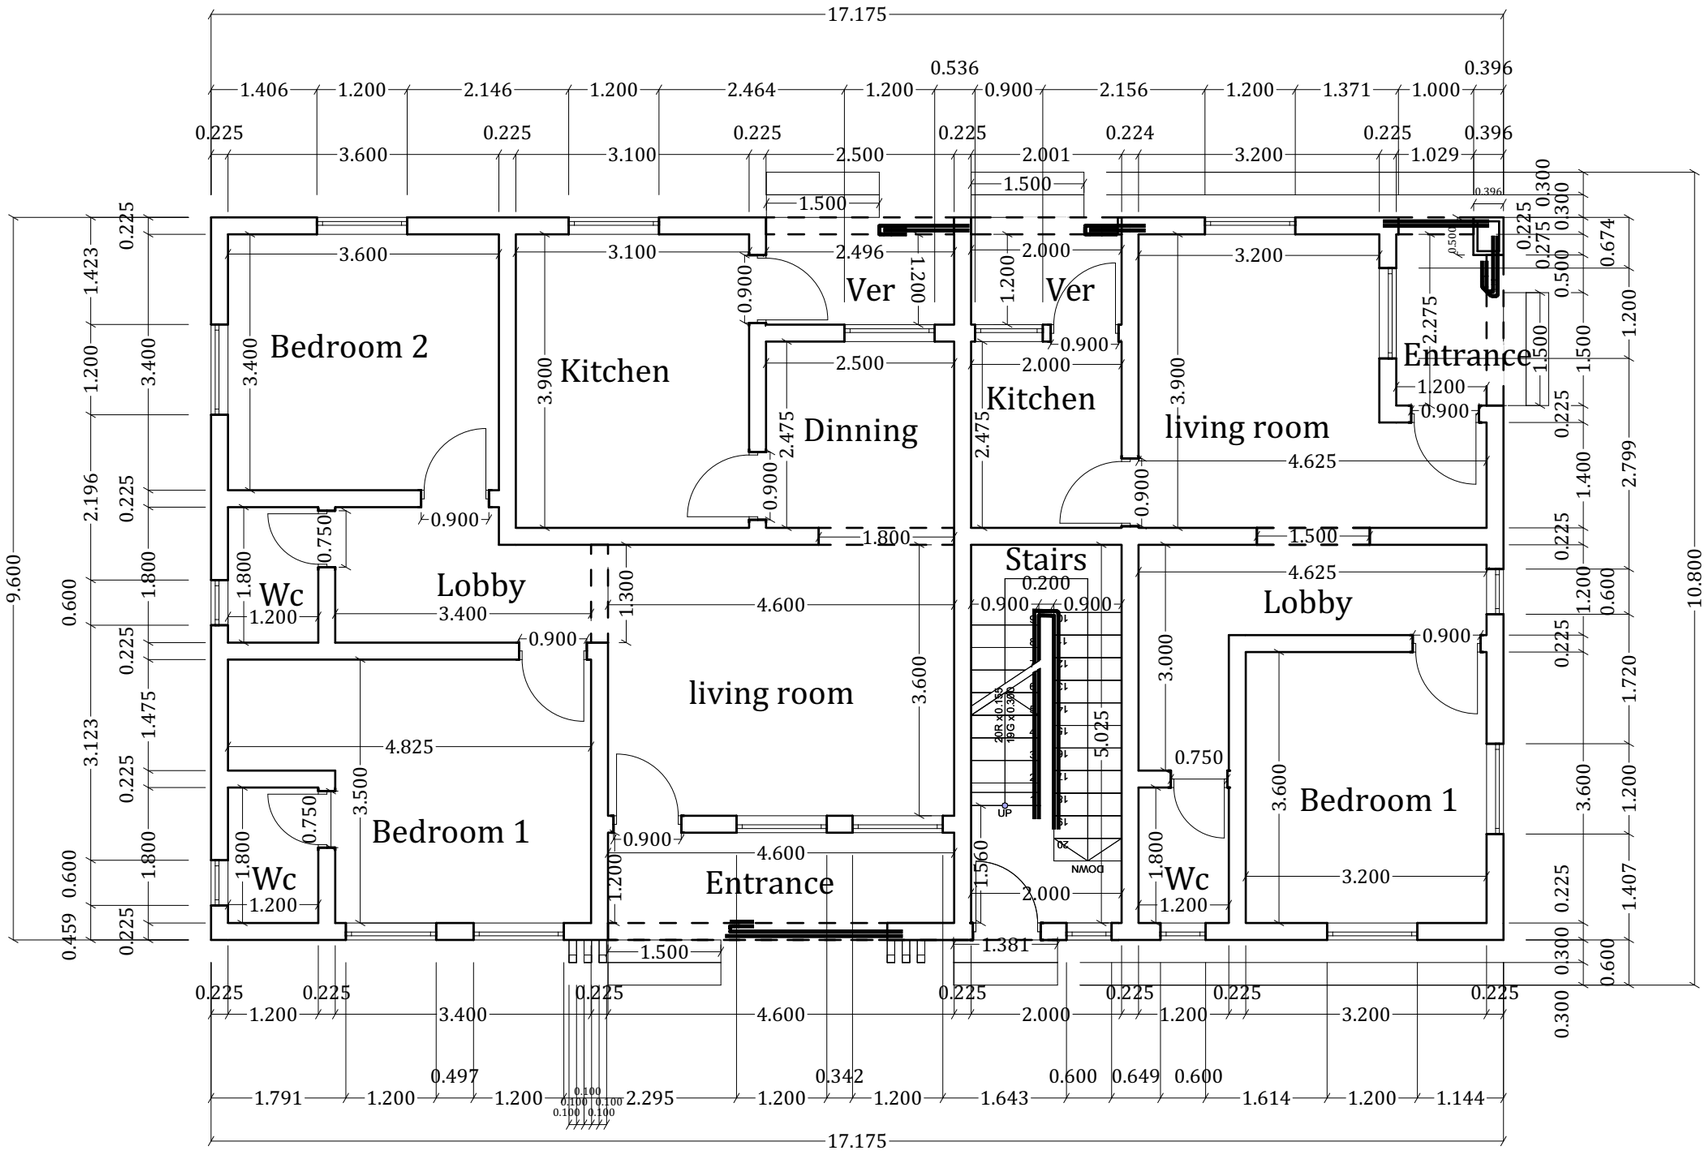



GROUND FLOOR PLAN

project: **3 UNITS OF FLAT**	Client: MR SUNDAY IDEGWU Location: ALAPERE KETU LAGOS STATE	Designed by: KELVIN IDEGWU Drawn by: KELVIN IDEGWU	Drawing title: GROUND FLOOR PLAN WORKING DRAWING Date: AUGUST 2025	All dimensions in meters and milimiters Scale: 1;100	1

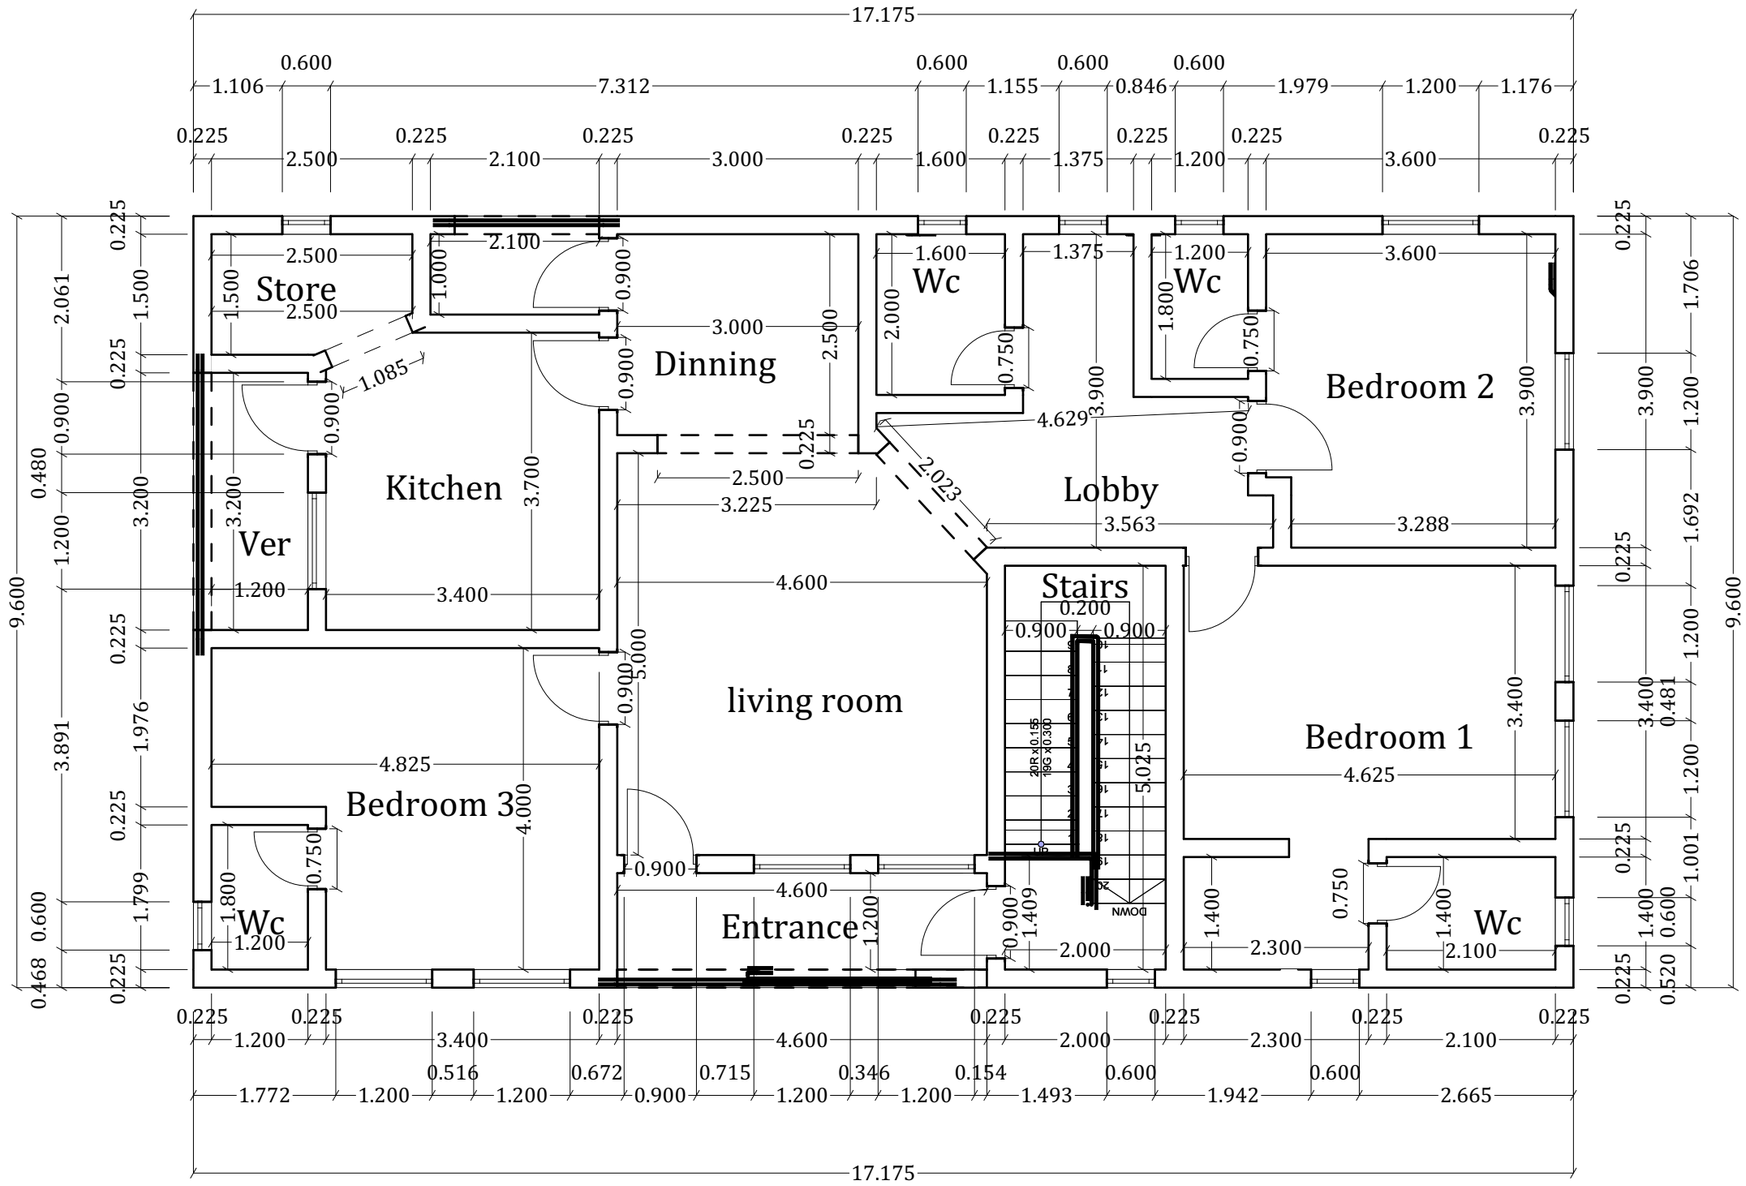

FIRST FLOOR PLAN

project: **3 UNITS OF FLAT**	Client: MR SUNDAY IDEGWU Location: ALAPERE KETU LAGOS STATE	Designed by: KELVIN IDEGWU Drawn by: KELVIN IDEGWU	Drawing title: FIRST FLOOR PLAN WORKING DRAWING Date: AUGUST 2025	All dimensions in meters and milimiters Scale: 1;100	2

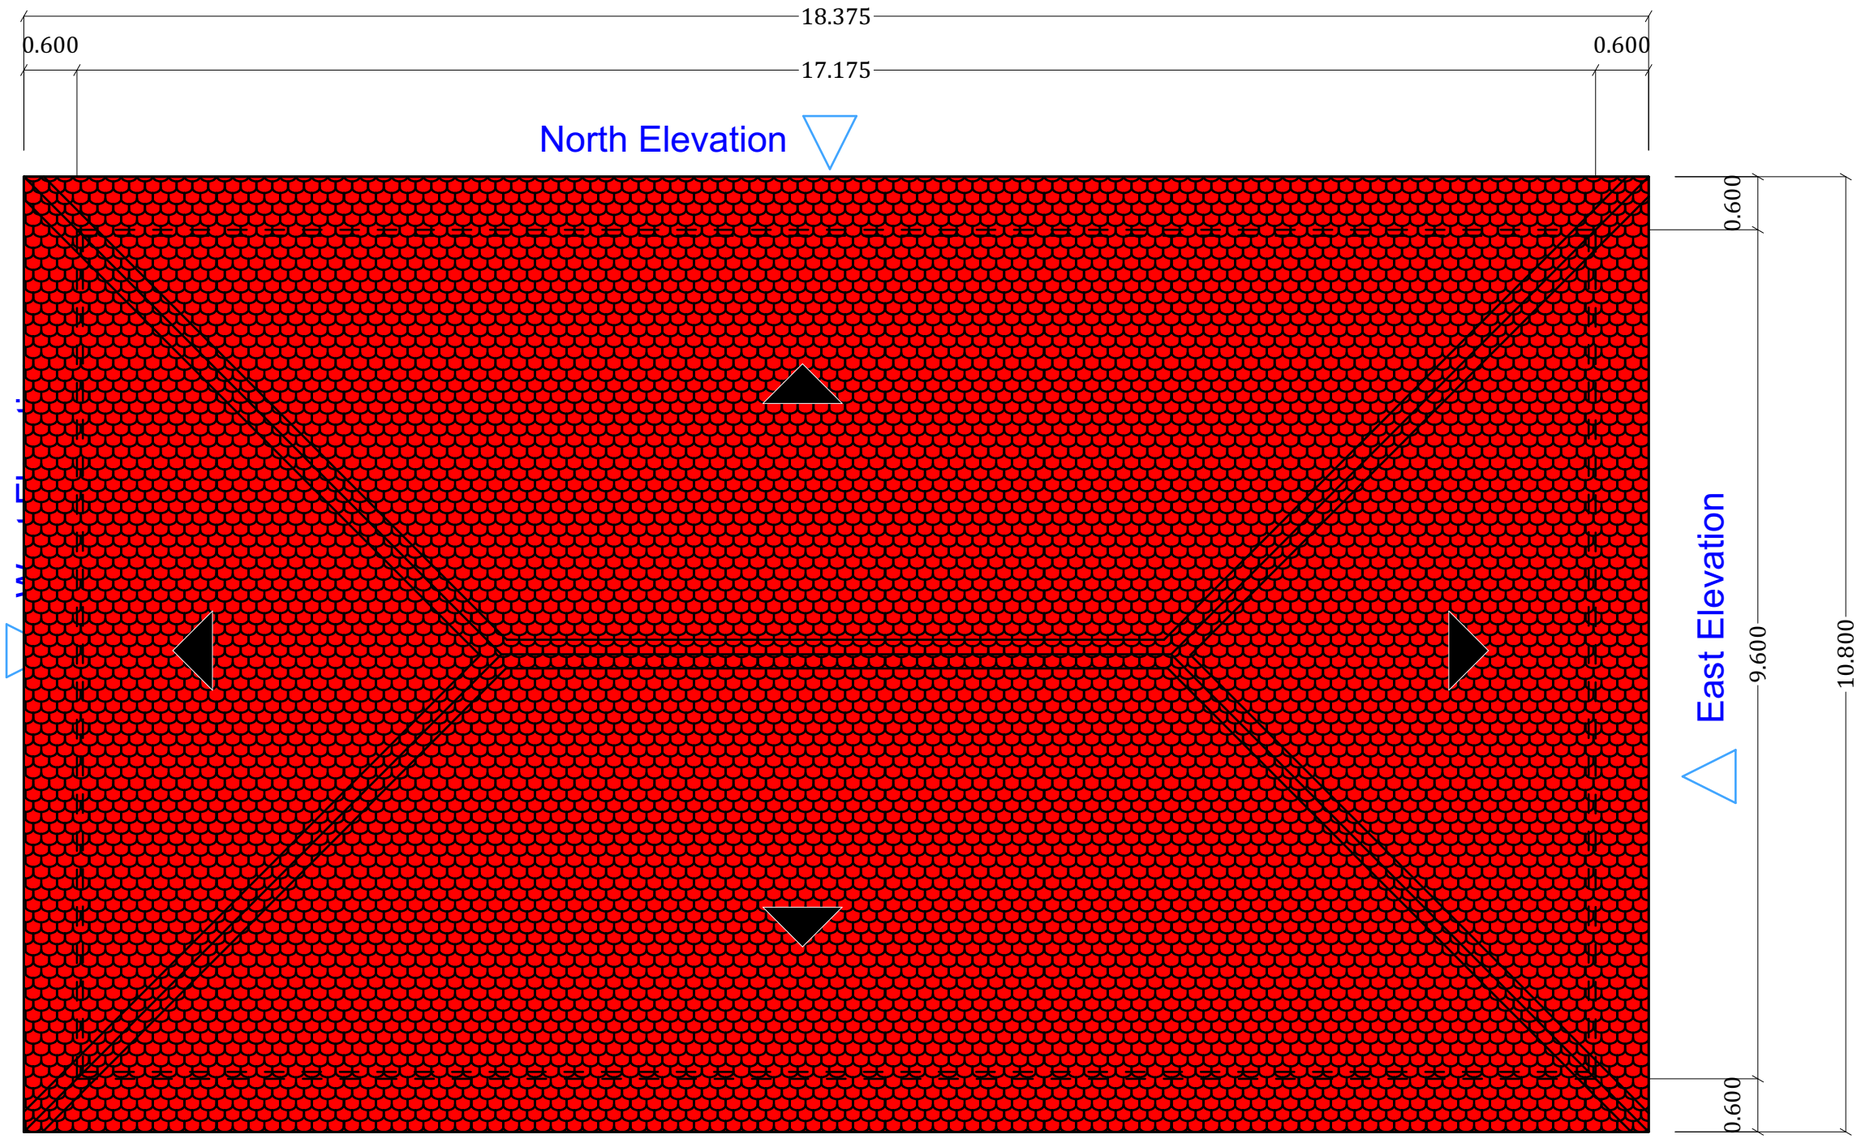

ROOF PLAN

project: **3 UNITS OF FLAT**	Client: MR SUNDAY IDEGWU Location: ALAPERE KETU LAGOS STATE	Designed by: KELVIN IDEGWU Drawn by: KELVIN IDEGWU	Drawing title: ROOF PLAN WORKING DRAWING Date: AUGUST 2025	All dimensions in meters and milimiters Scale: 1;100	3



FRONT ELEVATION



BACK ELEVATION

project:

3 UNITS OF FLAT

Client: MR SUNDAY IDEGWU

Location: ALAPERE KETU LAGOS STATE

Designed by: KELVIN IDEGWU

Drawn by: KELVIN IDEGWU

Drawing title: FRONT & BACK ELEVATION

WORKING DRAWING

Date: AUGUST 2025

All dimensions in meters and milimiters

Scale: 1;100

4



RIGHT ELEVATION



LEFT ELEVATION

project:

3 UNITS OF FLAT

Client: MR SUNDAY IDEGWU

Location: ALAPERE KETU LAGOS STATE

Designed by: KELVIN IDEGWU

Drawn by: KELVIN IDEGWU

Drawing title: RIGHT & LEFT ELEVATION

WORKING DRAWING

Date: AUGUST 2025

All dimensions in meters and milimiters

Scale: 1;100

5