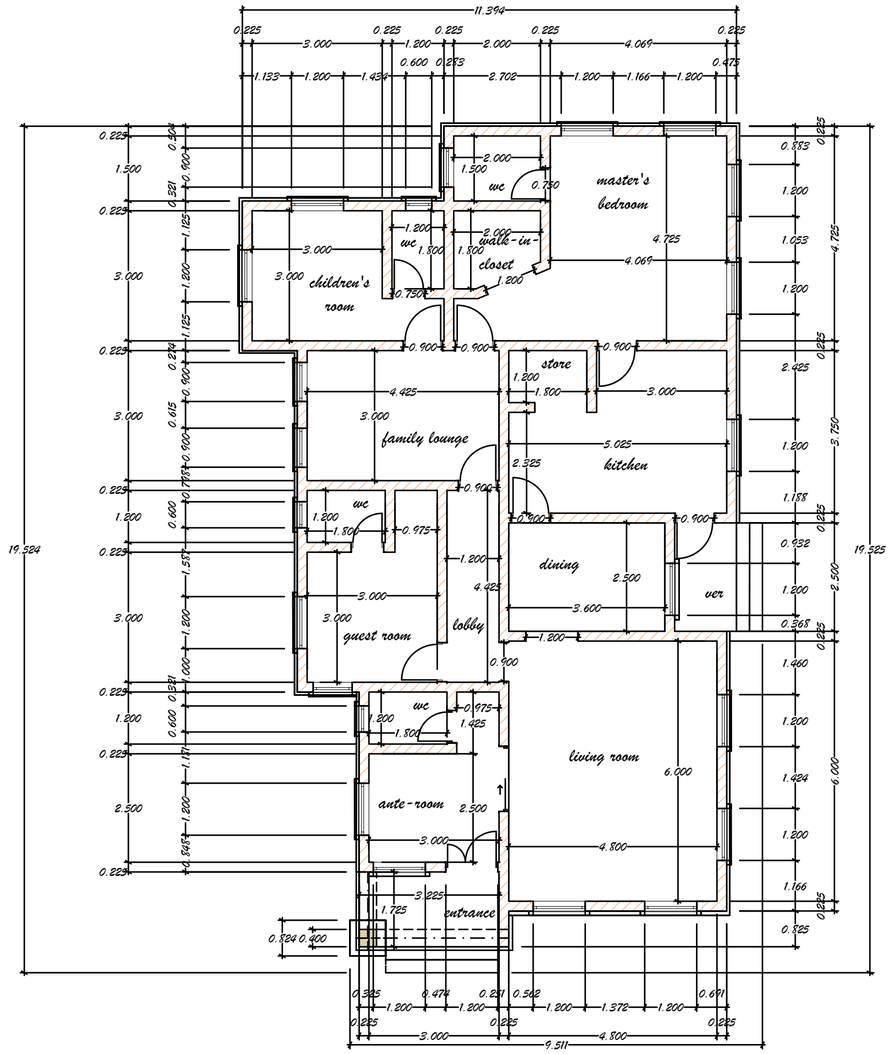



# FLOOR PLAN

Approval column:

Project:


## 3 BEDROOM BUNGALOW DESIGN

Client:

MR EMMANUEL IDEGWU

| | | | |
|---|---|---|---|
| Designed By: ARC. A. PRECIOUS | Drawing title: FLOOR PLAN | Date: JANUARY 2025 | Stamp: |
| Checked by: ARC. I. KELVIN | Signed By: ARC. I. KELVIN | Scale: 1:100 | Drawing No: 1 |

bringing your vision to life...
Estrella Design

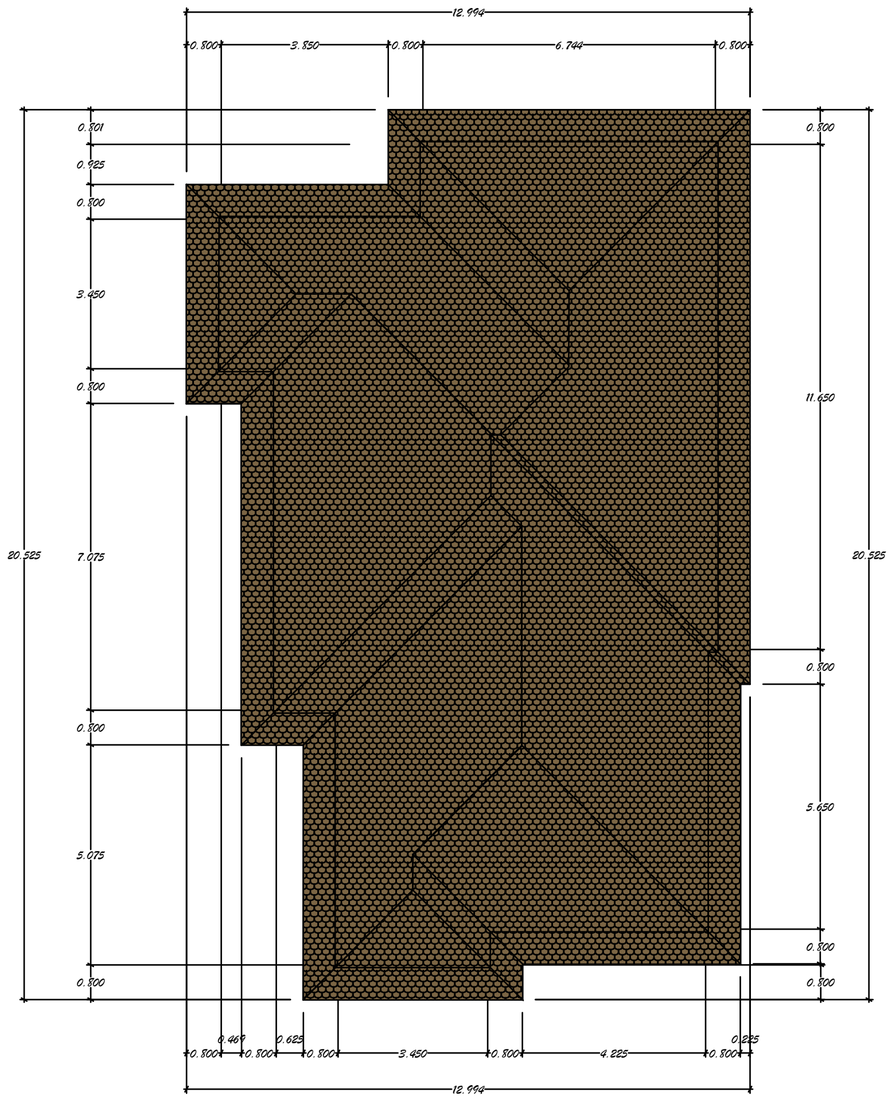


# ROOF PLAN

Approval column:

*Project:*

# 3 BEDROOM BUNGALOW DESIGN

*Client:*

MR EMMANUEL IDEGWU

Designed By:
**ARC A PRECIOUS**

Drawing title:
ROOF PLAN

Date:
**JANUARY 2025**

Scale:
*1:100*


Drawing No:
**2**

Checked by:
**ARC I KELVIN**


Signed By:
**ARC I KELVIN**

**N.T.S**

Stamp:

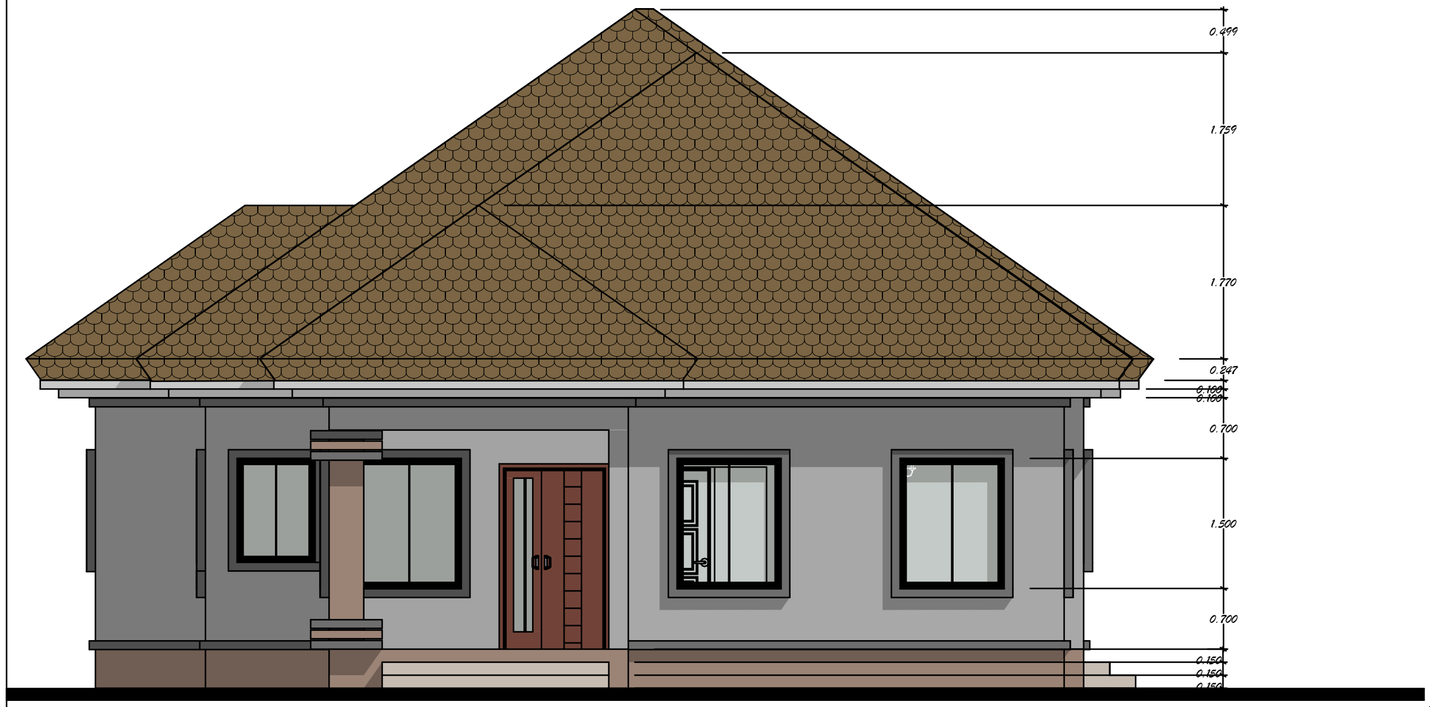


SOUTH ELEVATION

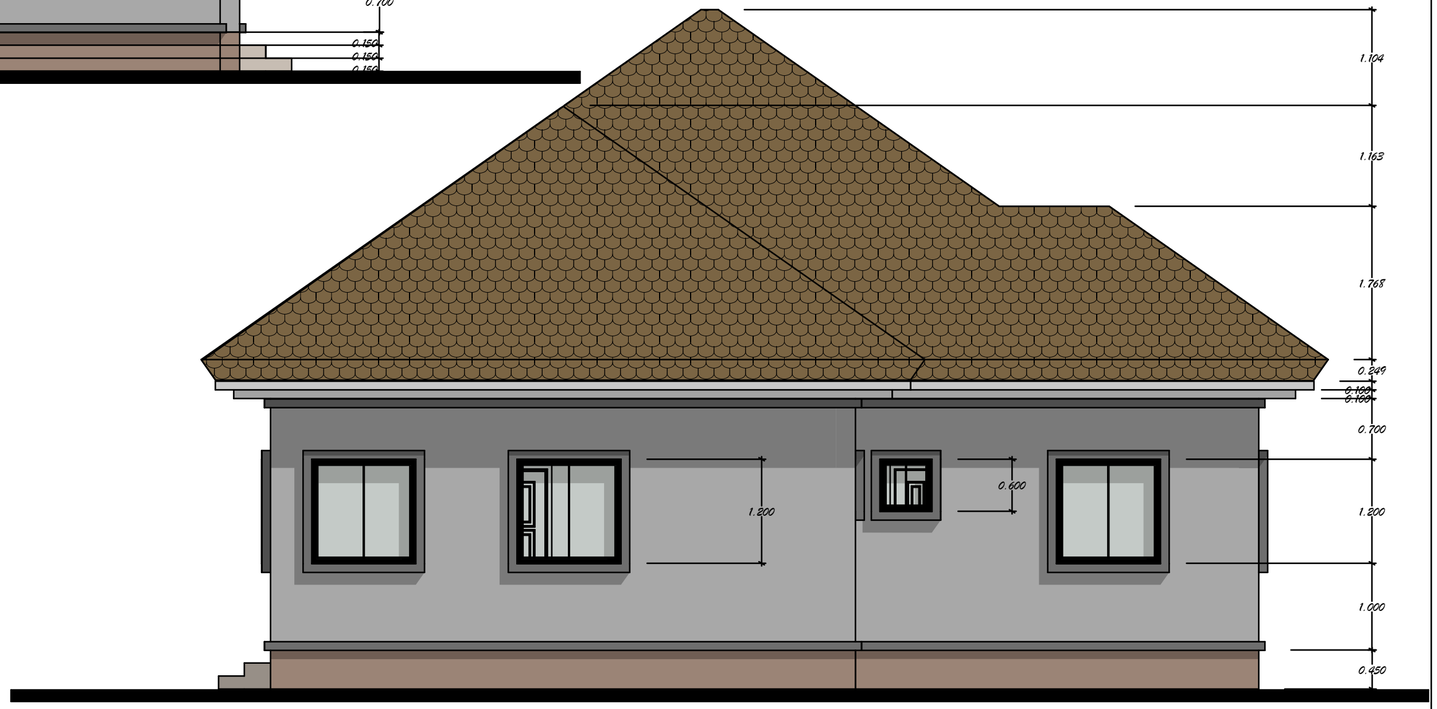


NORTH ELEVATION

Approval column:

Project:

# 3 BEDROOM BUNGALOW DESIGN

Client:

MR EMMANUEL IDEGWU

Designed By:
ARC A PRECIOUS

Drawing title:
SOUTH AND NORTH ELEVATION

Checked by:
ARC I KELVIN

Signed By:
ARC I KELVIN


Date:
JANUARY 2025

Scale:
1:100


N.T.S

Drawing No:
3

Stamp:

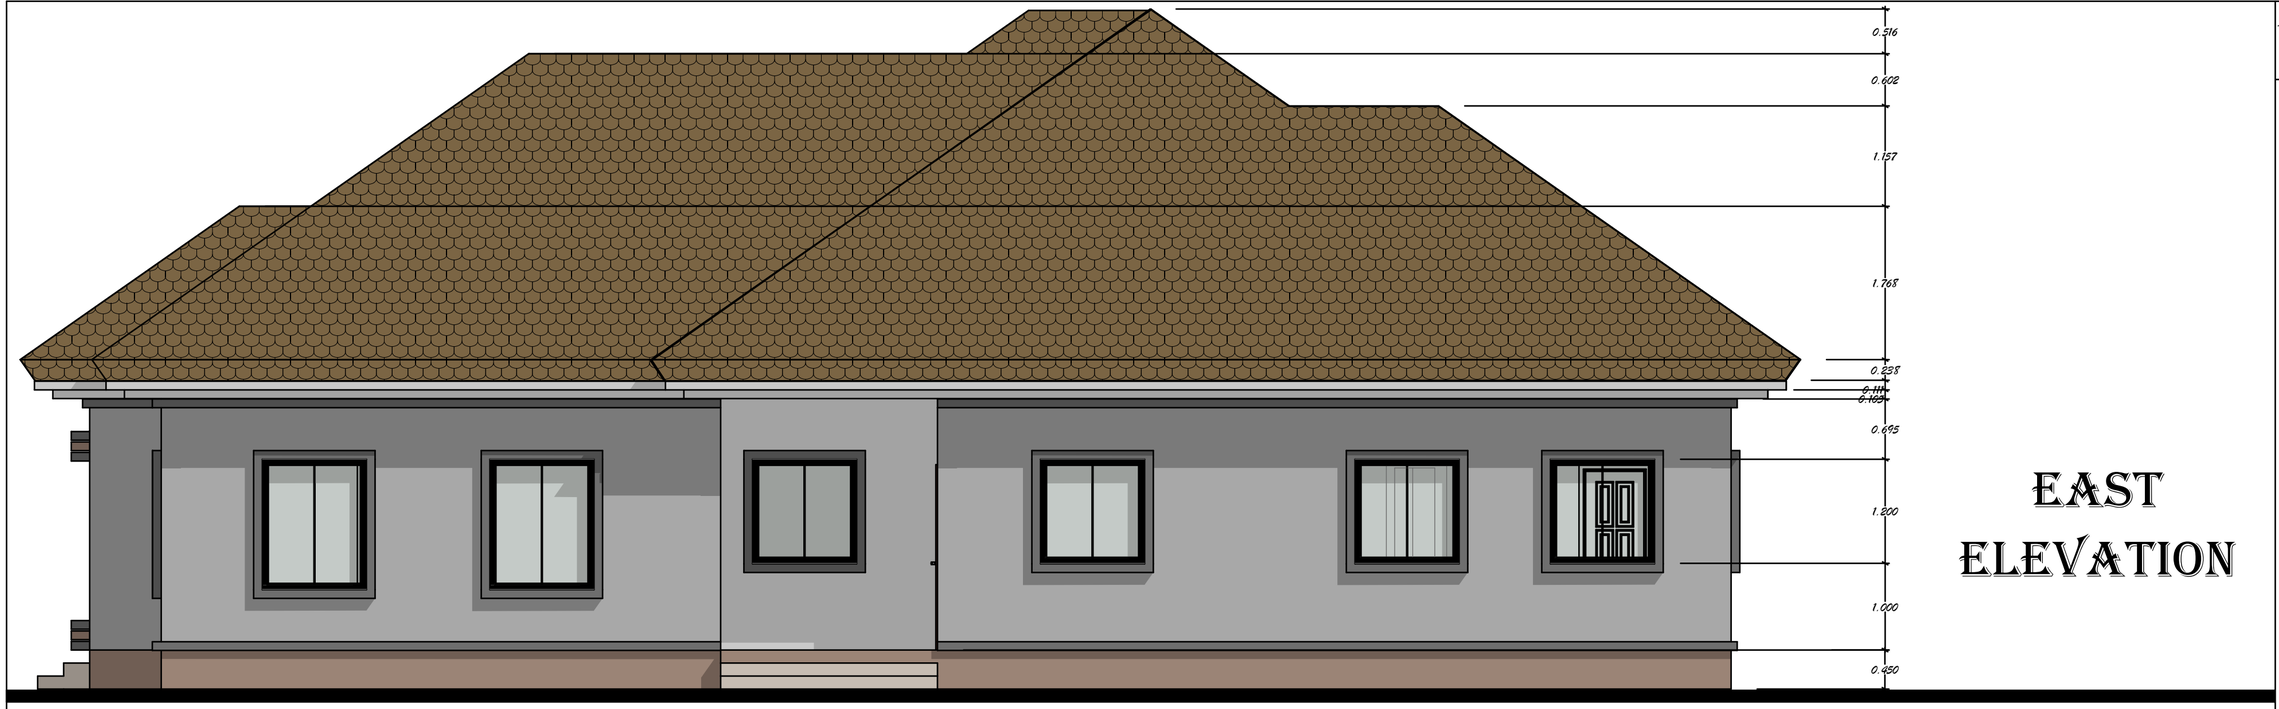


# EAST ELEVATION

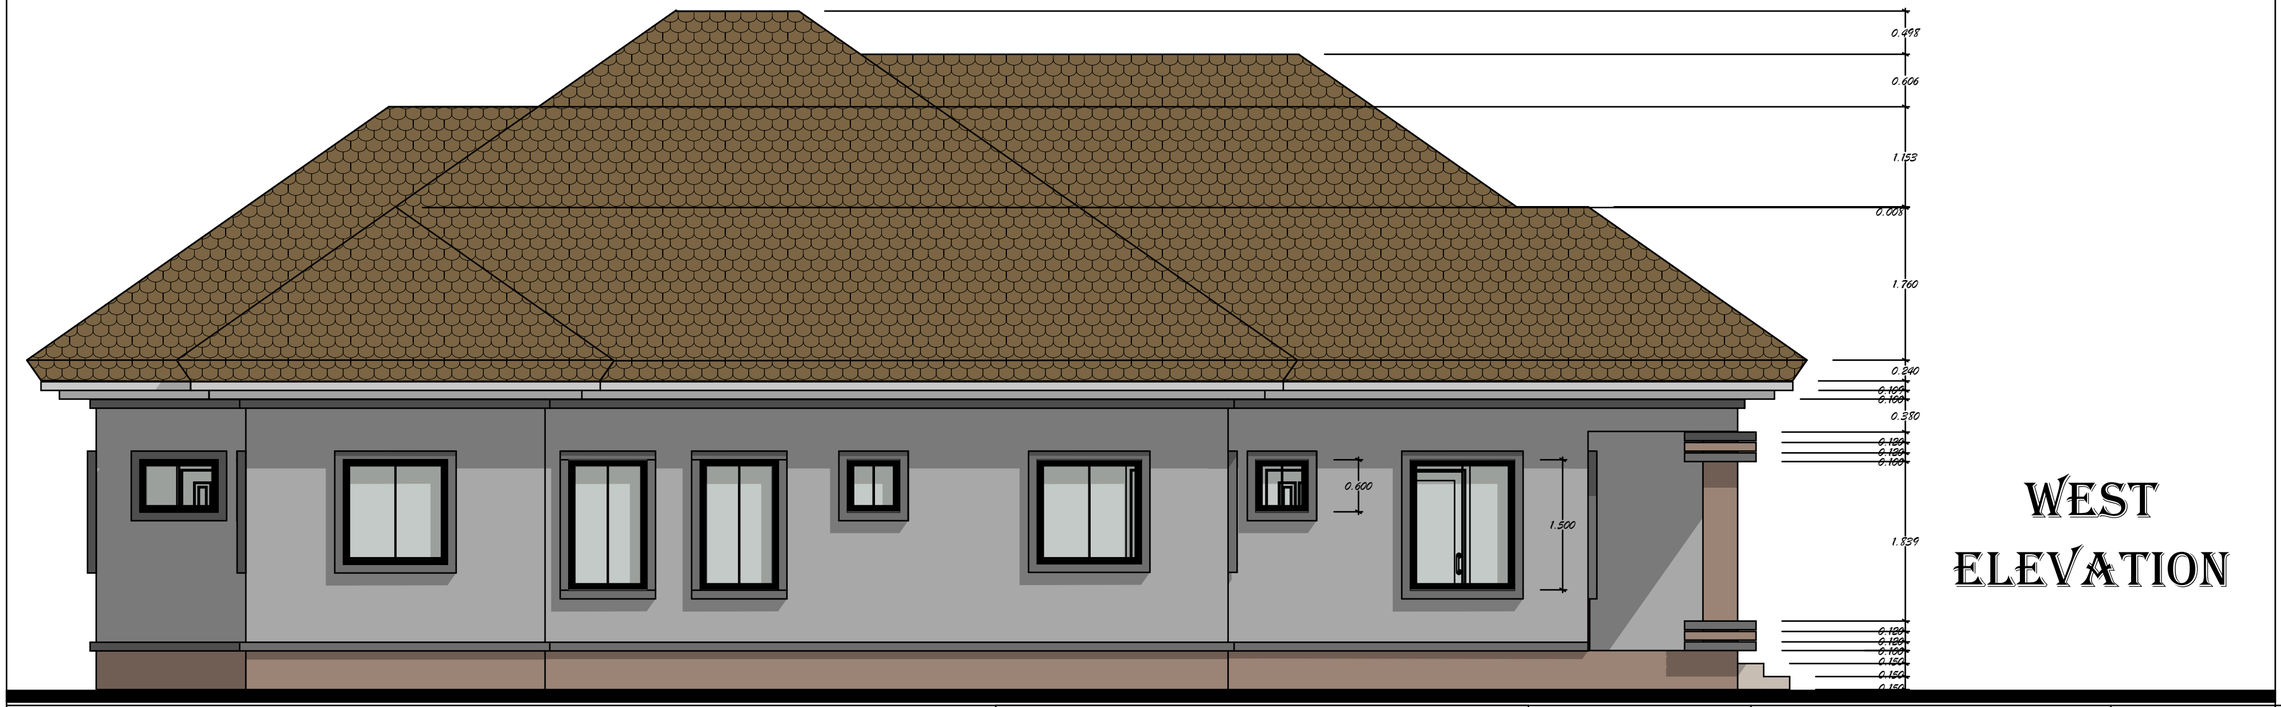


# WEST ELEVATION

Approval column:

Project:

# 3 BEDROOM BUNGALOW DESIGN

Client:

MR EMMANUEL IDEGWU

Designed By: ARC A PRECIOUS

Drawing title: EAST AND WEST ELEVATION

Date: JANUARY 2025

Scale: 1:100

Drawing No: 4

Checked by: ARC I KELVIN

Signed By: ARC I KELVIN

N.T.S

Stamp: