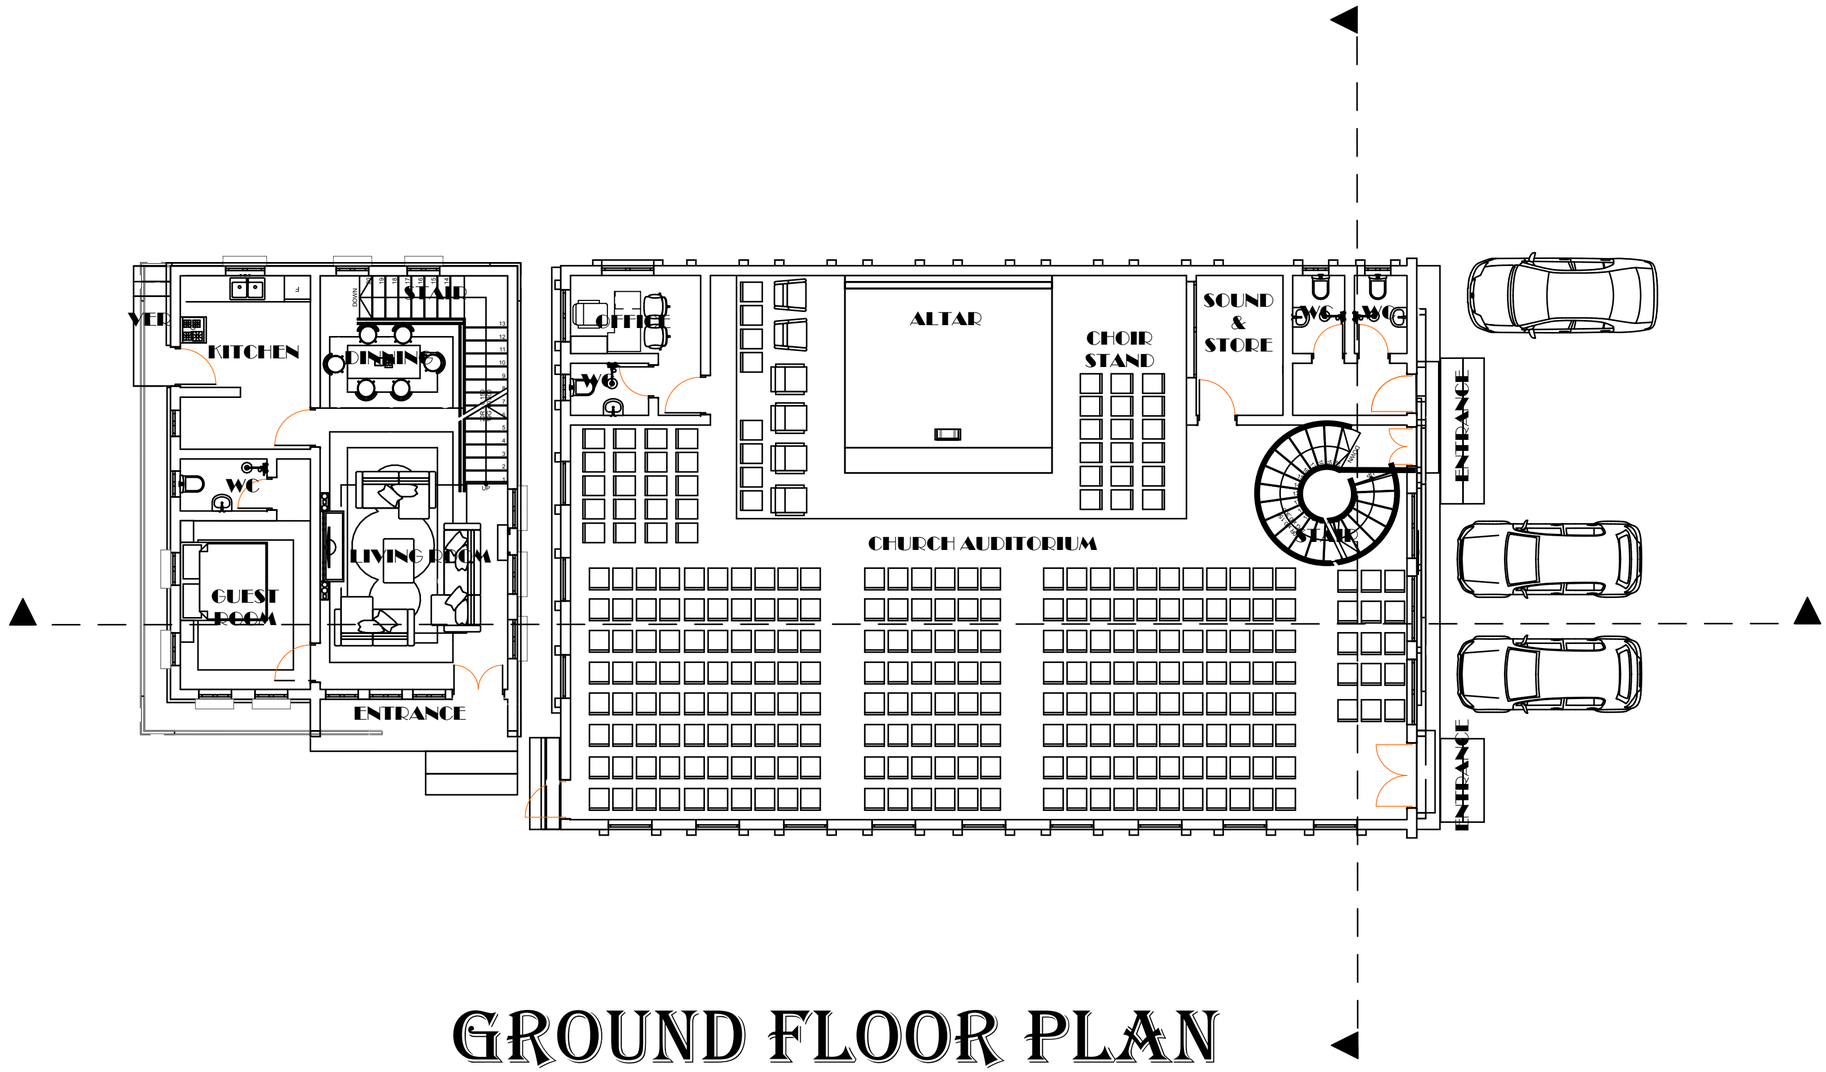


GROUND FLOOR PLAN

PROJECT DETAILS

Project name:CHURCH/PASTOR'S RESIDENCE
Location:Off Murutauv Olorunfemi street Egan Lagos, Nigeria.
Client:Jesus Restoration Covenant Church Of God.
Designed:Estrella Design
Drawn:Estrella Design

DRAWING DETAILS & DATE

Units: Meters (m) and Millimeters (mm)
Scale:1:100
Date: July 2024

SHEET INFORMATION


Sheet title: GROUND FLOOR PLAN

GENERAL NOTES

*All dimensions in meters and millimeters except otherwise stated
*All dimensions to be read and scaled of drawings.
*All dimensions to be feild verified.
*Errors,discripancies or ommission to be reported.
*Queries must be clarified before any work commences.
*Contractor liable for correct setting out of points, levels and heights with particular reference to bundaries,building lines and external/internal walls.

bringing your vision to life...
Estrella Design

Sheet Number
1

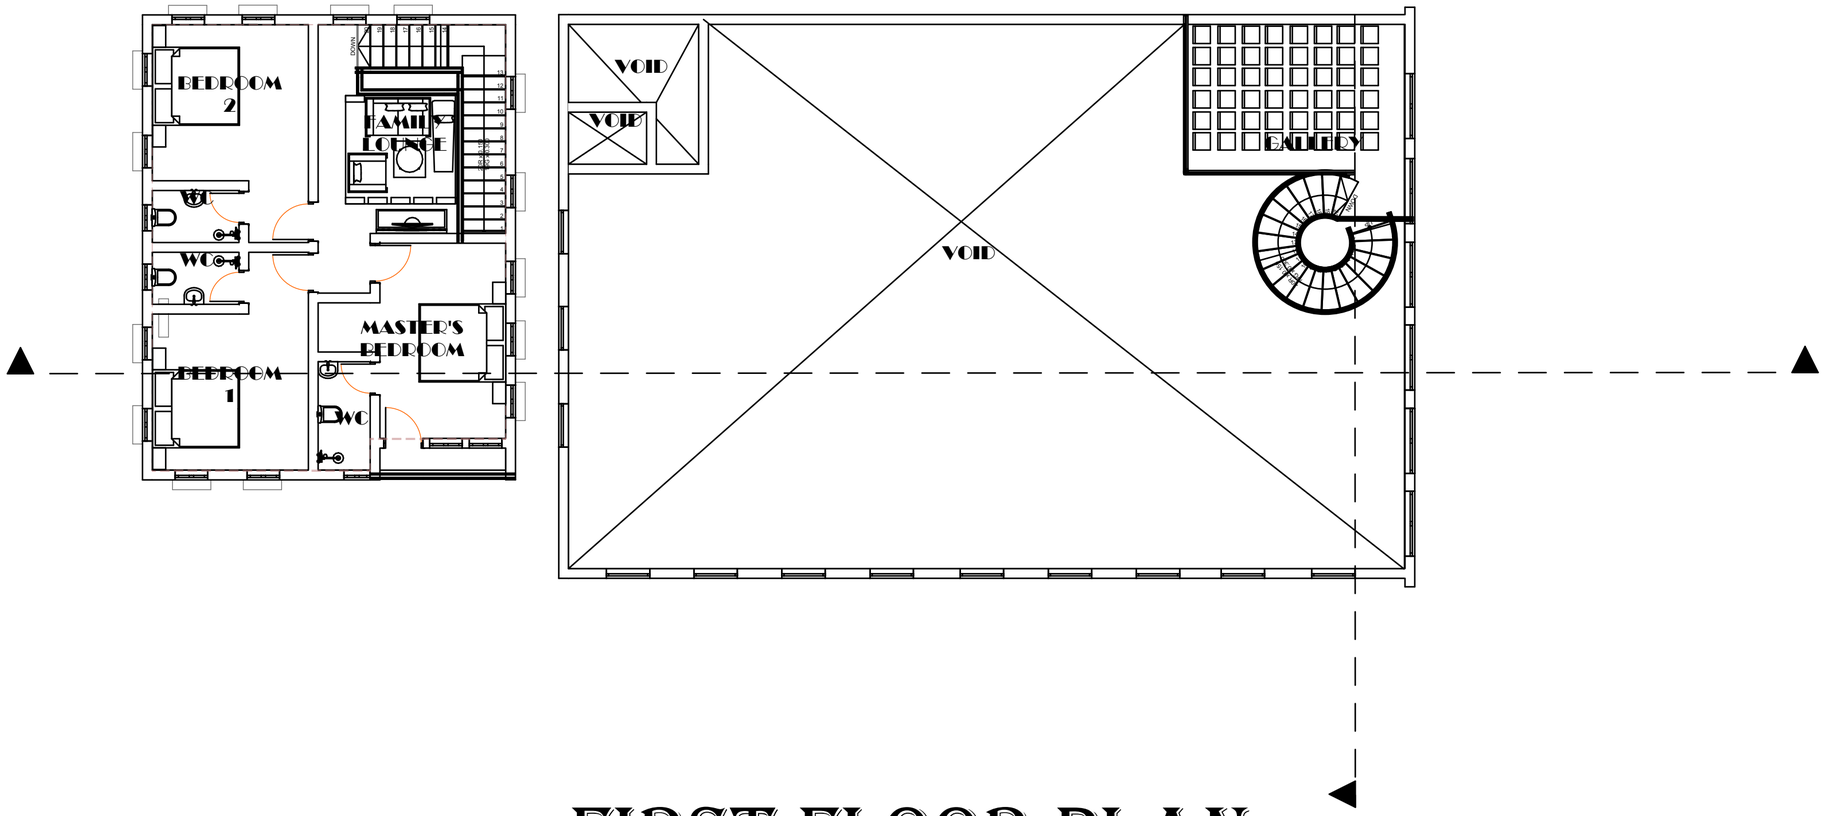

FIRST FLOOR PLAN

PROJECT DETAILS

Project name:CHURCH/PASTOR'S RESIDENCE
Location:Off Murutauv Olorunfemi street Egan Lagos, Nigeria.
Client:Jesus Restoration Covenant Church Of God.
Designed:Estrella Design
Drawn:Estrella Design

DRAWING DETAILS & DATE

Units: Meters (m) and Millimeters (mm)
Scale:1:100
Date: July 2024

SHEET INFORMATION


Sheet title: FIRST FLOOR PLAN

GENERAL NOTES

*All dimensions in meters and millimeters except otherwise stated
*All dimensions to be read and scaled of drawings.
*All dimensions to be feild verified.
*Errors,discripancies or ommission to be reported.
*Queries must be clarified before any work commences.
*Contractor liable for correct setting out of points, levels and heights with particular reference to bundaries,building lines and external/internal walls.

bringing your vision to life...
Estrella Design

Sheet Number
2

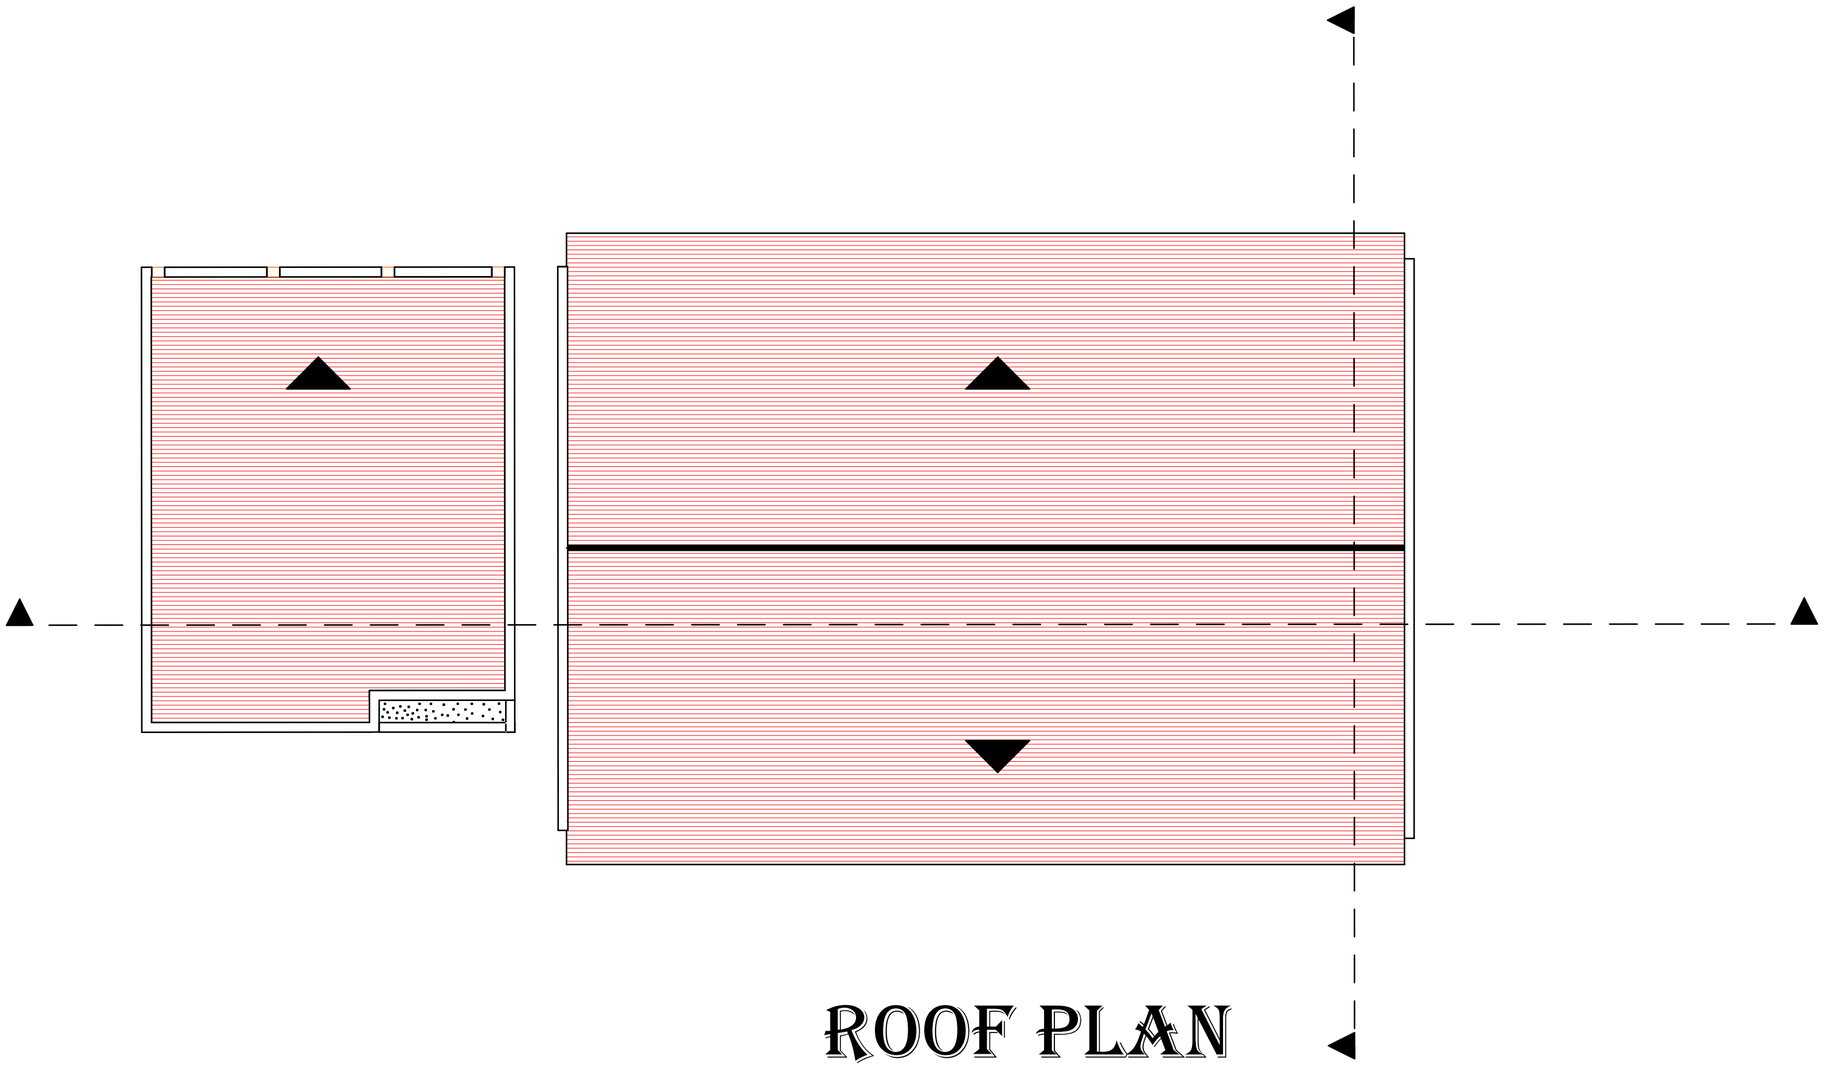

ROOF PLAN

PROJECT DETAILS

Project name:CHURCH/PASTOR'S RESIDENCE
Location:Off Murutauv Olorunfemi street Egan Lagos, Nigeria.
Client:Jesus Restoration Covenant Church Of God.
Designed:Estrella Design
Drawn:Estrella Design

DRAWING DETAILS & DATE

Units: Meters (m) and Millimeters (mm)
Scale:1:100
Date: July 2024

SHEET INFORMATION

Sheet title: ROOF PLAN


GENERAL NOTES

*All dimensions in meters and millimeters except otherwise stated
*All dimensions to be read and scaled of drawings.
*All dimensions to be feild verified.
*Errors,discripancies or ommission to be reported.
*Queries must be clarified before any work commences.
*Contractor liable for correct setting out of points, levels and heights with particular reference to bundaries,building lines and external/internal walls.


bringing your vision to life...
Estrella Design

Sheet Number

3

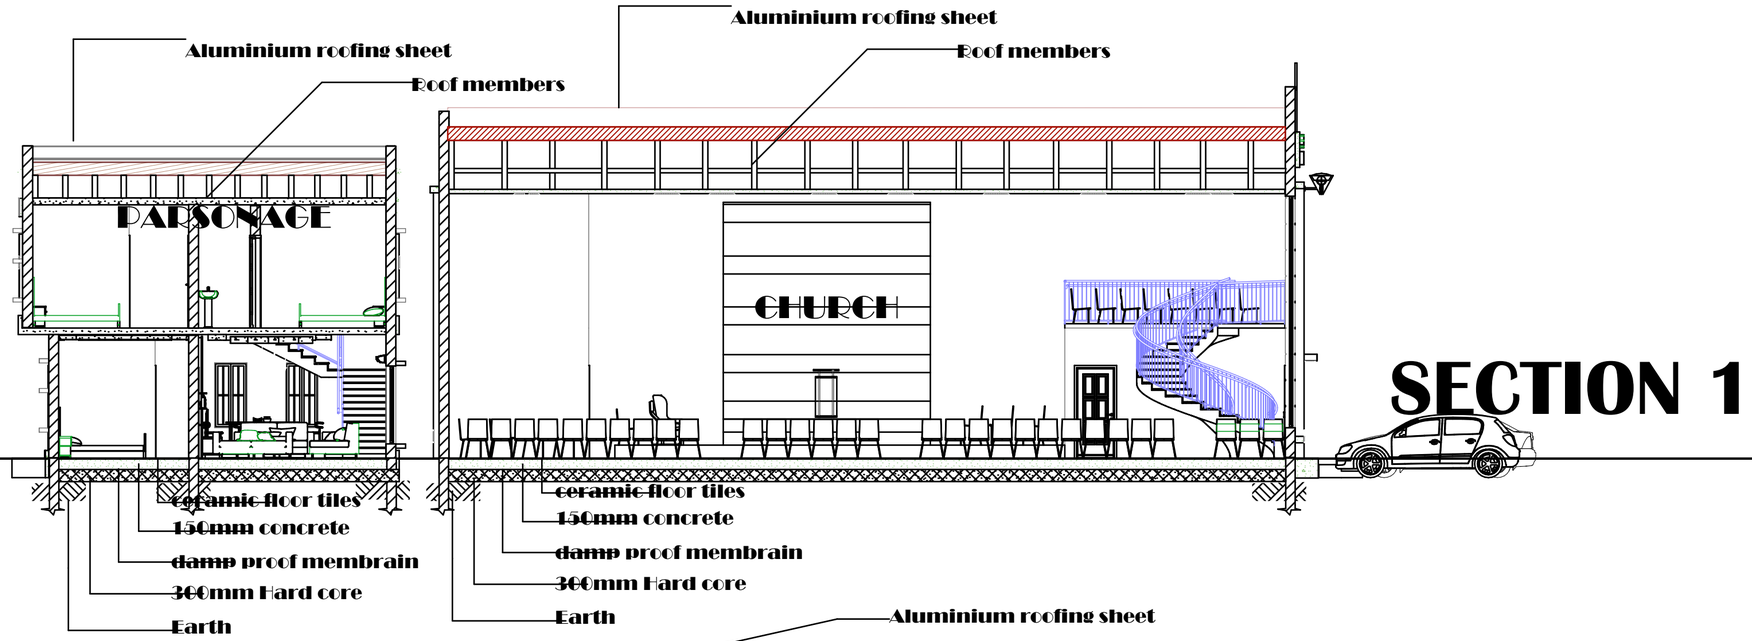

SECTION 1

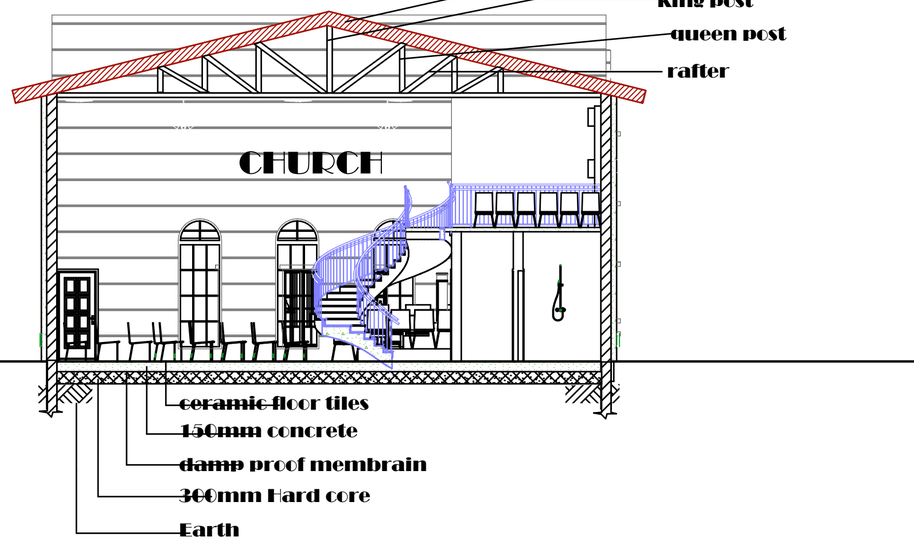

SECTION 2

PROJECT DETAILS

- Project name:CHURCH/PASTOR'S RESIDENCE
- Location:Off Murutauv Olorunfemi street Egan Lagos, Nigeria.
- Client:Jesus Restoration Covenant Church Of God.
- Designed:Estrella Design
- Drawn:Estrella Design

DRAWING DETAILS & DATE

- Units: Meters (m) and Millimeters (mm)
- Scale:1:100
- Date: July 2024

SHEET INFORMATION


Sheet title: SECTIONS

GENERAL NOTES

*All dimensions in meters and millimeters except otherwise stated
*All dimensions to be read and scaled of drawings.
*All dimensions to be feild verified.
*Errors,discripancies or ommission to be reported.
*Queries must be clarified before any work commences.
*Contractor liable for correct setting out of points, levels and heights with particular reference to bundaries,building lines and external/internal walls.

bringing your vision to life...
Estrella Design

Sheet Number
7

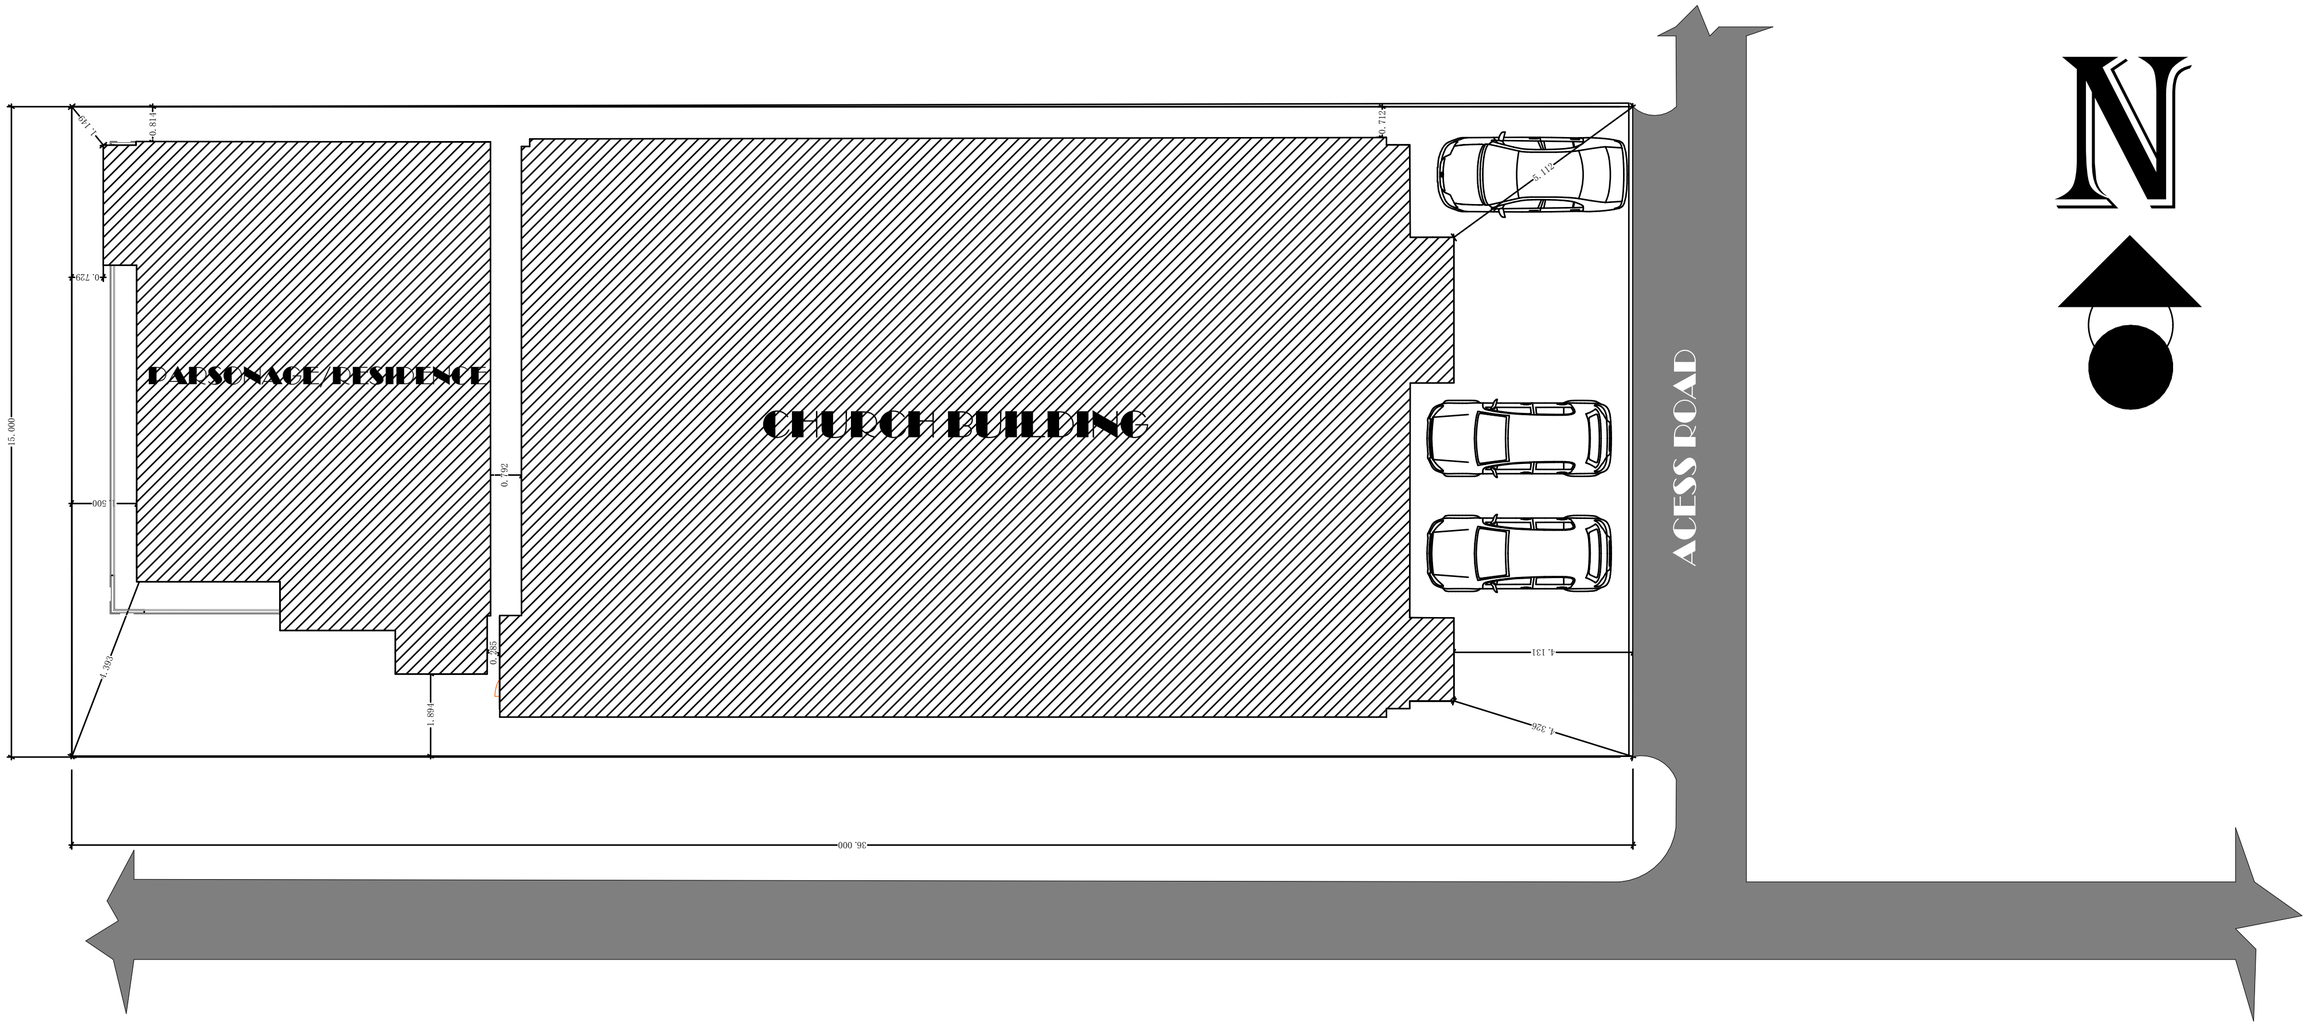

SITE PLAN

PROJECT DETAILS

Project name:CHURCH/PASTOR'S RESIDENCE
Location:Off Murutauv Olorunfemi street Egan Lagos, Nigeria.
Client:Jesus Restoration Covenant Church Of God.
Designed:Estrella Design
Drawn:Estrella Design

DRAWING DETAILS & DATE

Units: Meters (m) and Millimeters (mm)
Scale:1:100
Date: July 2024

SHEET INFORMATION

Sheet title: SITE PLAN

GENERAL NOTES


*All dimensions in meters and millimeters except otherwise stated
*All dimensions to be read and scaled of drawings.
*All dimensions to be feild verified.
*Errors,discripancies or ommission to be reported.
*Queries must be clarified before any work commences.
*Contractor liable for correct setting out of points, levels and heights with particular reference to bundaries,building lines and external/internal walls.

bringing your vision to life...
Estrella Design

Sheet Number
8



SOUTH ELEVATION

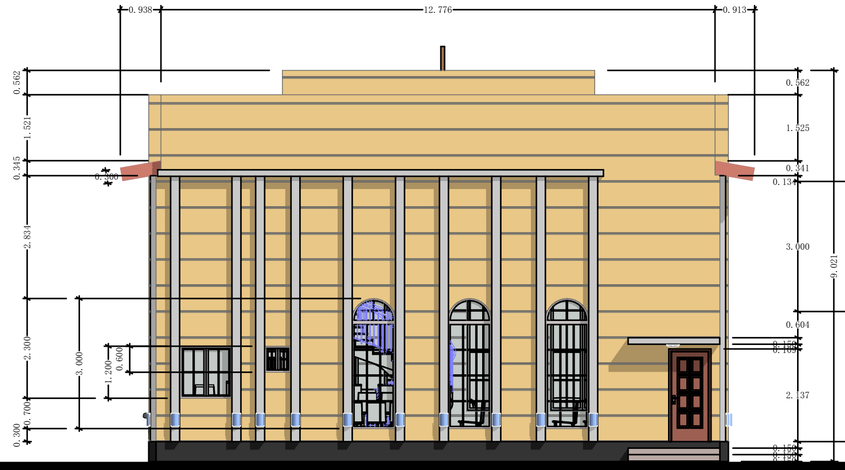

NORTH ELEVATION

PROJECT DETAILS

Project name:CHURCH/PASTOR'S RESIDENCE
Location:Off Murutauv Olorunfemi street Egan Lagos, Nigeria.
Client:Jesus Restoration Covenant Church Of God.
Designed:Estrella Design
Drawn:Estrella Design

DRAWING DETAILS & DATE

Units: Meters (m) and Millimeters (mm)
Scale:1:100
Date: July 2024

SHEET INFORMATION

Sheet title: SOUTH AND NORTH ELEVATION


GENERAL NOTES

*All dimensions in meters and millimeters except otherwise stated
*All dimensions to be read and scaled of drawings.
*All dimensions to be feild verified.
*Errors,discripancies or ommission to be reported.
*Queries must be clarified before any work commences.
*Contractor liable for correct setting out of points, levels and heights with particular reference to bundaries,building lines and external/internal walls.


bringing your vision to life...
Estrella Design

Sheet Number

4

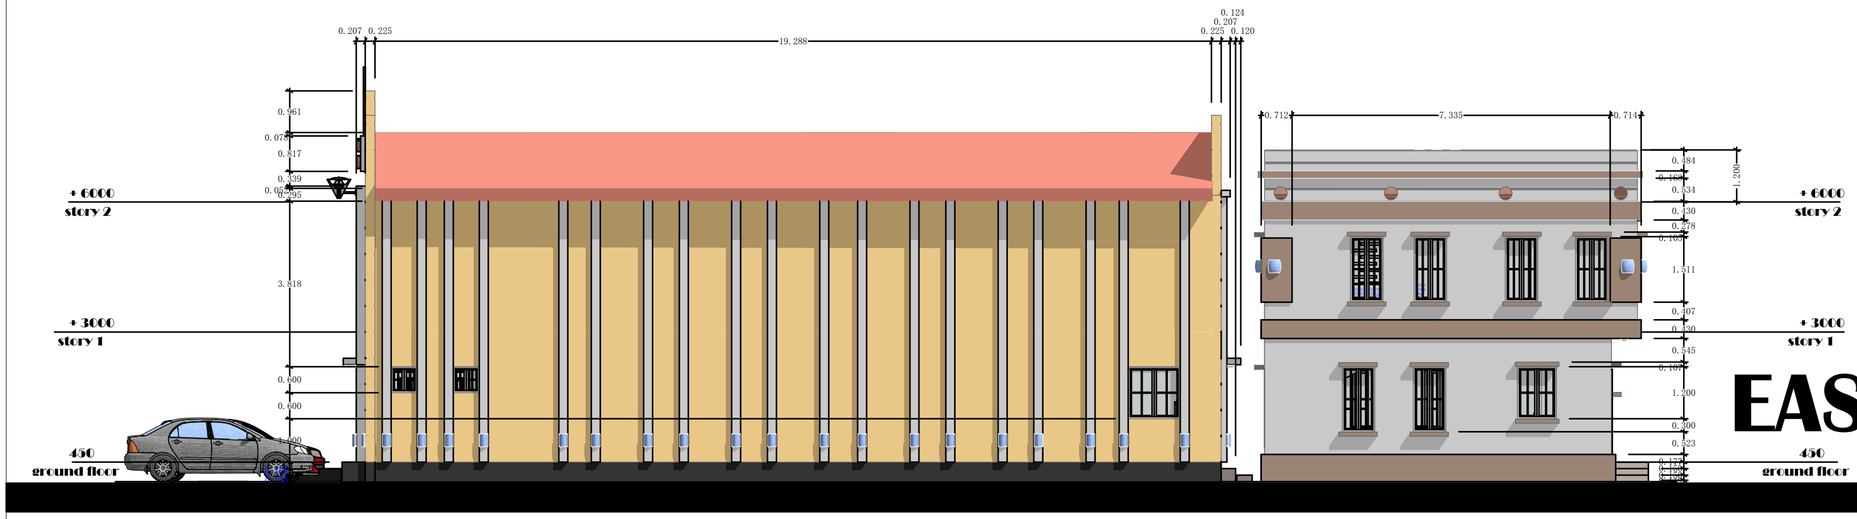

EAST ELEVATION

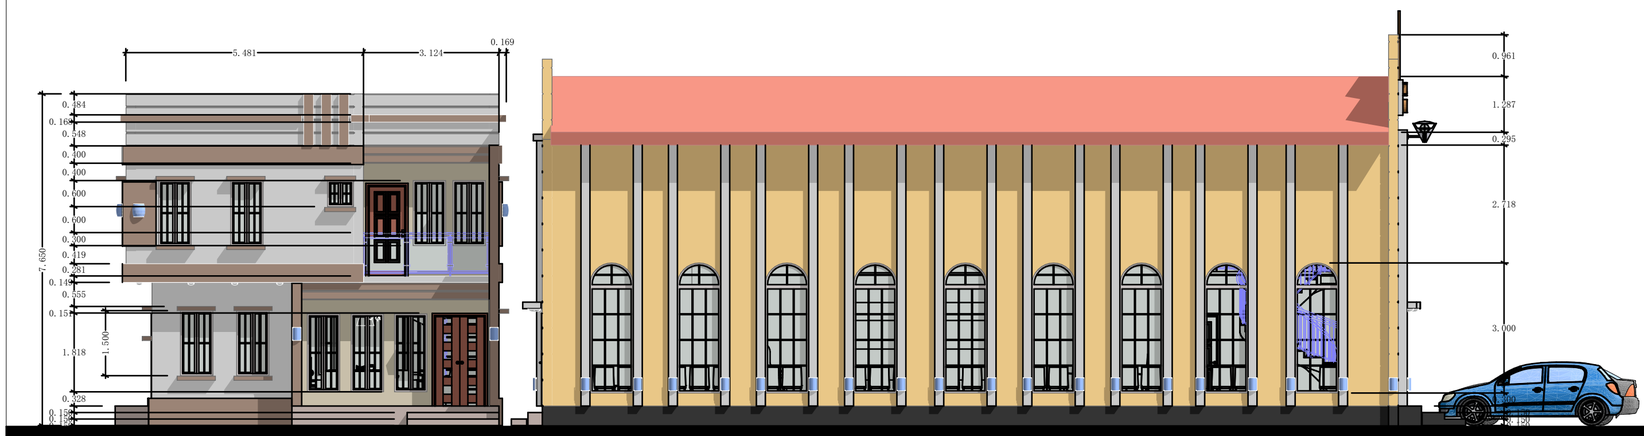

WEST ELEVATION

PROJECT DETAILS

- Project name:CHURCH/PASTOR'S RESIDENCE
- Location:Off Murutauv Olorunfemi street Egan Lagos, Nigeria.
- Client:Jesus Restoration Covenant Church Of God.
- Designed:Estrella Design
- Drawn:Estrella Design

DRAWING DETAILS & DATE

- Units: Meters (m) and Millimeters (mm)
- Scale:1:100
- Date: July 2024

SHEET INFORMATION

Sheet title: EAST AND WEST ELEVATION

GENERAL NOTES

*All dimensions in meters and millimeters except otherwise stated
*All dimensions to be read and scaled of drawings.
*All dimensions to be feild verified.
*Errors,discripancies or ommission to be reported.
*Queries must be clarified before any work commences.
*Contractor liable for correct setting out of points, levels and heights with particular reference to bundaries,building lines and external/internal walls.

bringing your vision to life...
Estrella Design

Sheet Number
5



SOUTH ELEVATION

+ 6000
story 2

+ 3000
story 1

450
ground floor



NORTH ELEVATION

+ 6000
story 2

+ 3000
story 1

450
ground floor

PROJECT DETAILS

Project name:CHURCH/PASTOR'S RESIDENCE
Location:Off Murutauv Olorunfemi street Egan Lagos, Nigeria.
Client:Jesus Restoration Covenant Church Of God.
Designed:Estrella Design
Drawn:Estrella Design

DRAWING DETAILS & DATE

Units: Meters (m) and Millimeters (mm)
Scale:1:100
Date: July 2024

SHEET INFORMATION

Sheet title: SOUTH AND NORTH ELEVATION

GENERAL NOTES

*All dimensions in meters and millimeters except otherwise stated
*All dimensions to be read and scaled of drawings.
*All dimensions to be feild verified.
*Errors,discripancies or ommission to be reported.
*Queries must be clarified before any work commences.
*Contractor liable for correct setting out of points, levels and heights with particular reference to bundaries,building lines and external/internal walls.

bringing your vision to life...
Estrella Design

Sheet Number
4