
Project Title: **MULTIPURPOSE HALL AND 3 BEDROOM APARTMENT DESIGN**


Designed by:	*Client:*	*Scale:*
AKOROGIE PRECIOUS	MR ANDREW	1:100
Drawn by:	*Date:*	
AKOROGIE PRECIOUS	August, 2025	



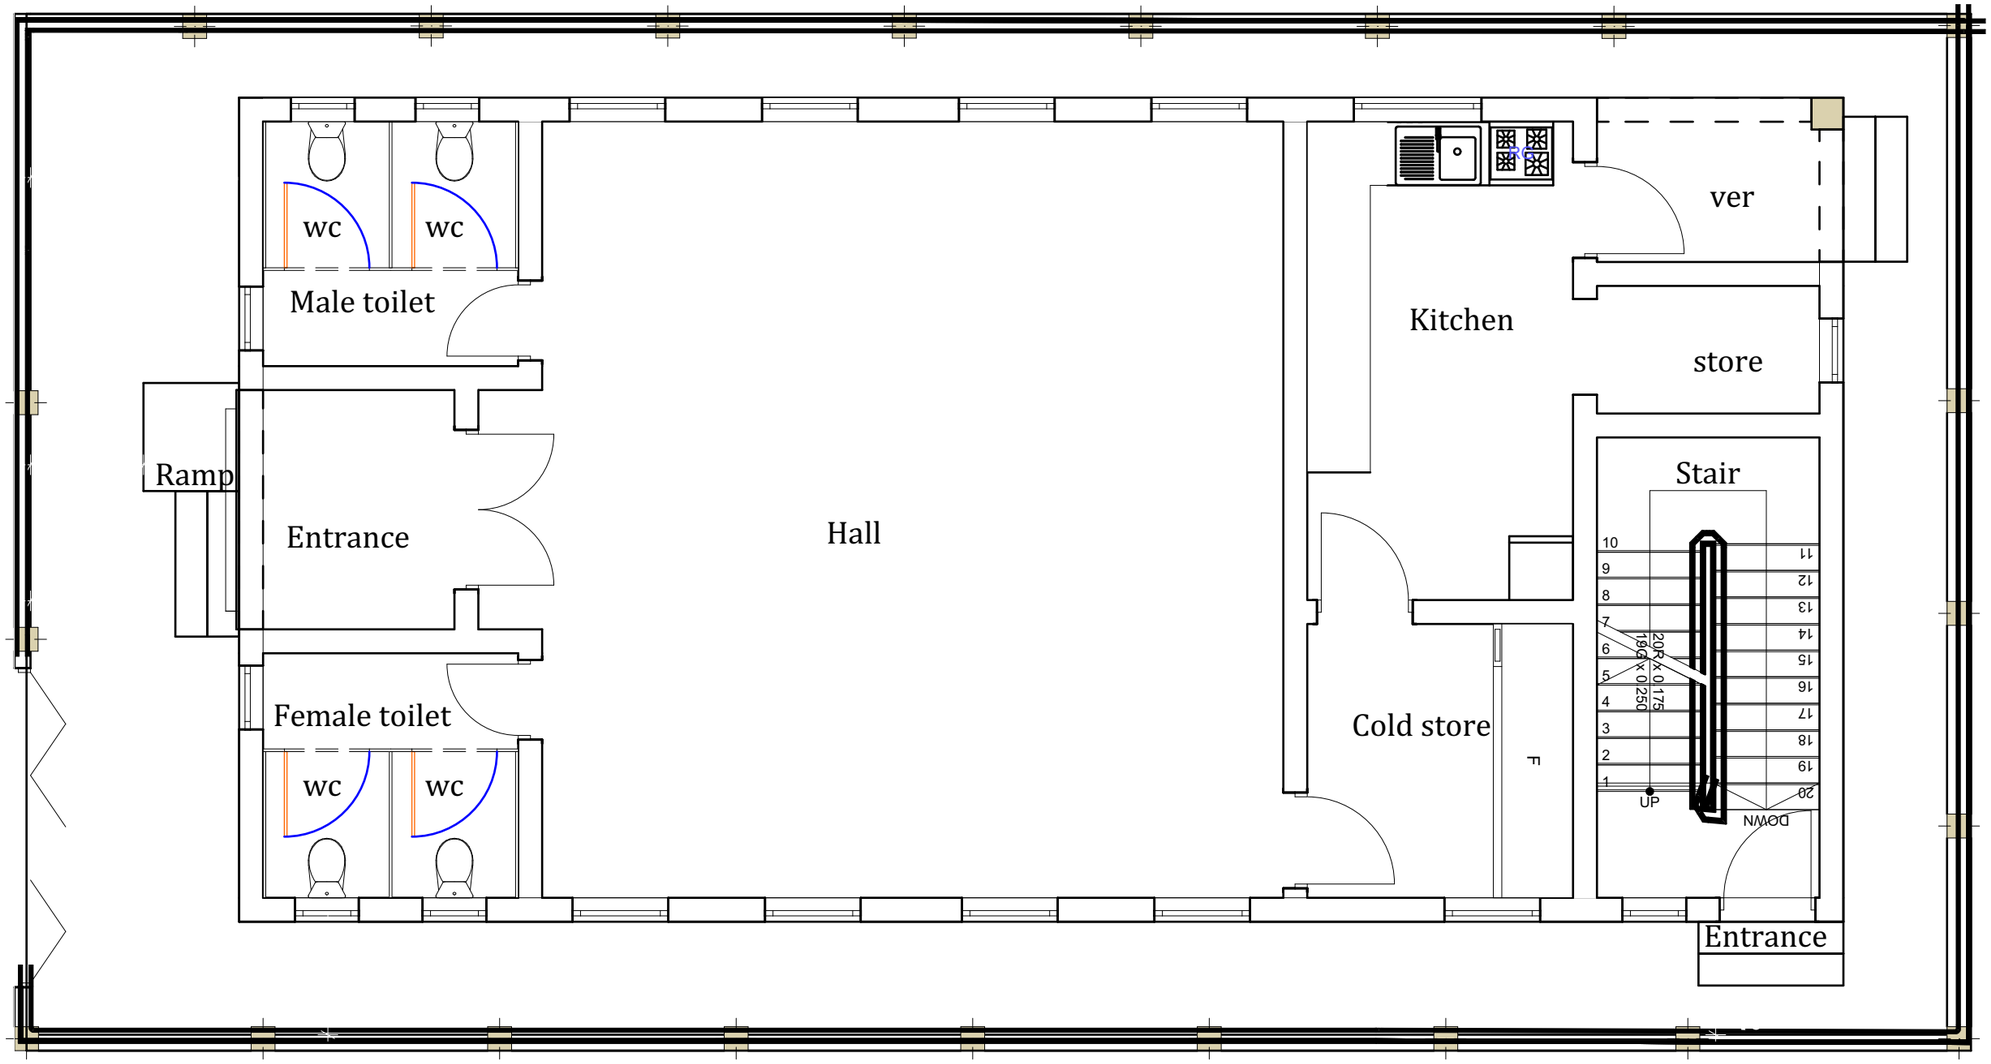

Project Title: **DINNING HALL AND THREE BEDROOM APARTMENT**	Estrella Design	*Designed by:* AKOROGIE PRECIOUS	*Client:* MR ANDREW	*Sheet Title:* Ground floor plan
		Drawn by: AKOROGIE PRECIOUS	*Scale:* 1:100	*Date:* August, 2025


Sheet Number: 6

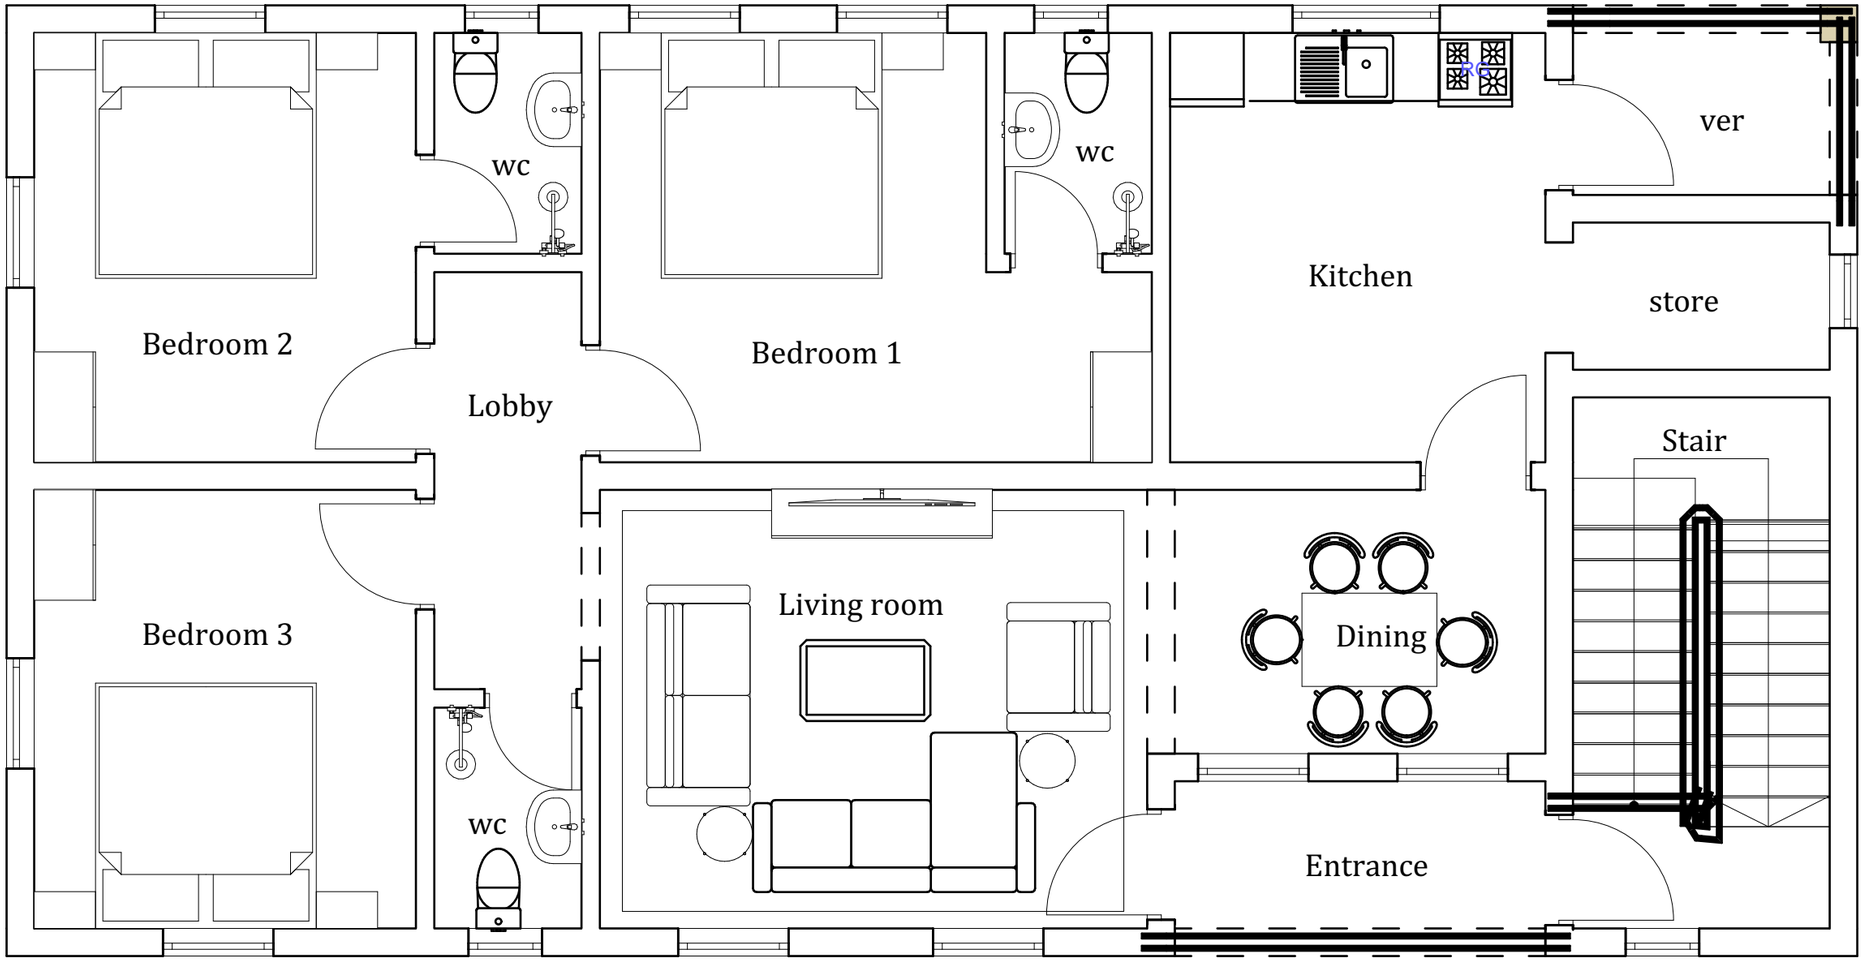

Project Title: **DINNING HALL AND THREE BEDROOM APARTMENT**		*Designed by:* AKOROGIE PRECIOUS	*Client:* MR ANDREW	*Sheet Title:* First floor plan
		Drawn by: AKOROGIE PRECIOUS	*Scale:* 1:100	*Date:* August, 2025

bringing your vision to life...
Estrella Design

Sheet Number: 7

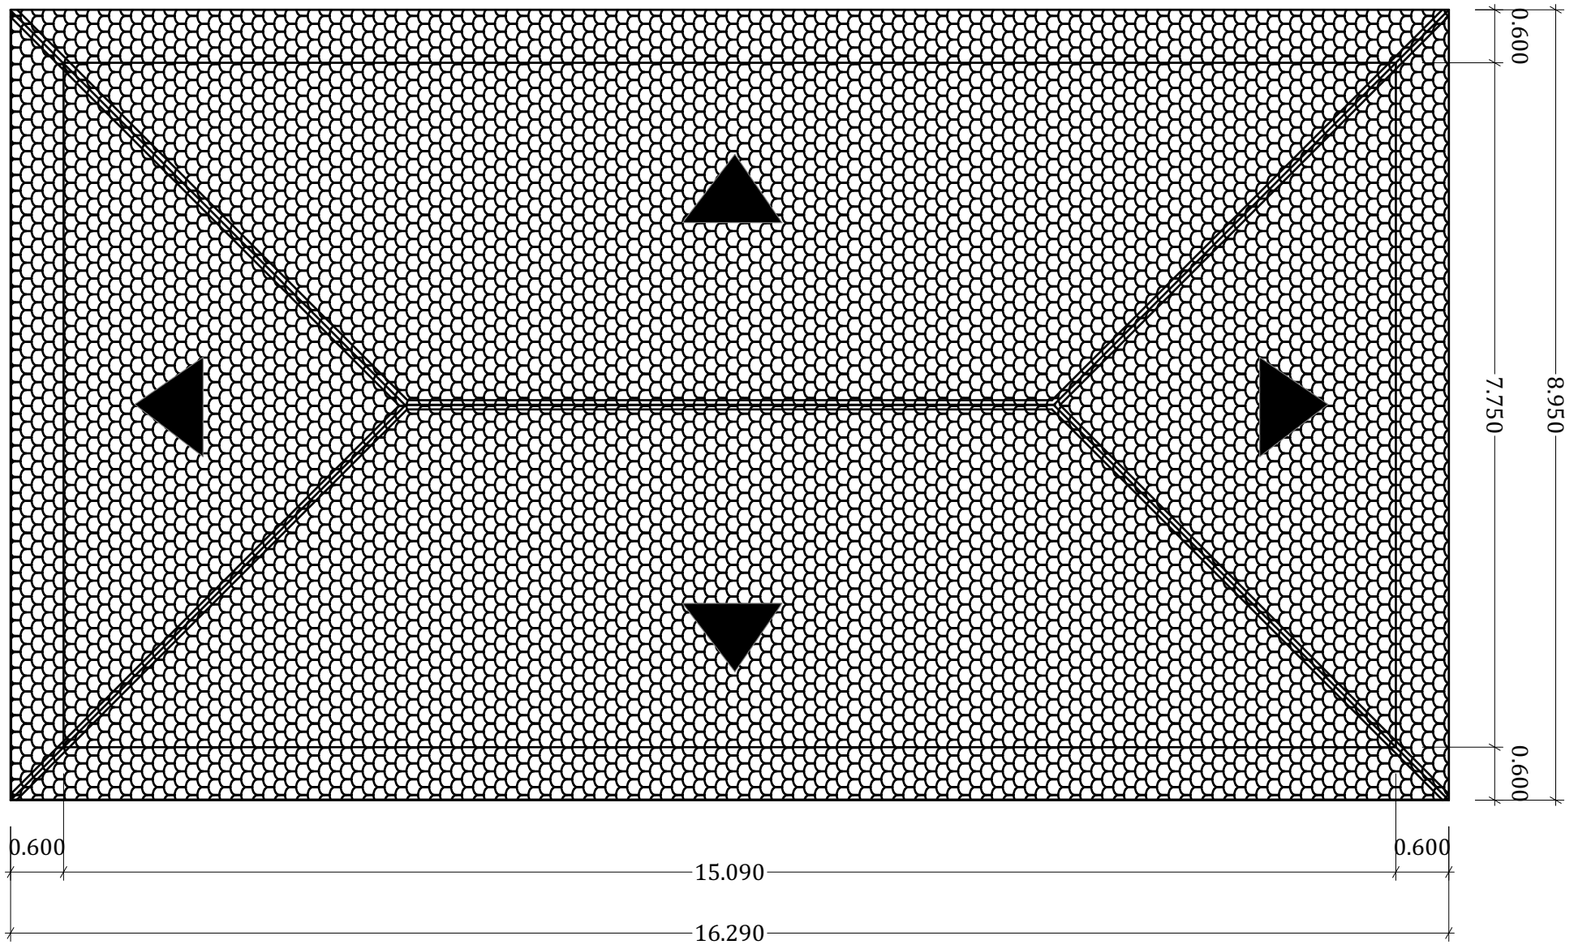


Project Title: **MULTIPURPOSE HALL AND 3 BEDROOM APARTMENT**		*Designed by:* AKOROGIE PRECIOUS	*Client:* MR ANDREW	*Sheet Title:* **Roof Plan**
		Drawn by: AKOROGIE PRECIOUS	*Scale:* 1:100	*Date:* August, 2025

bringing your vision to life...
Estrella Design

Sheet Number: 3



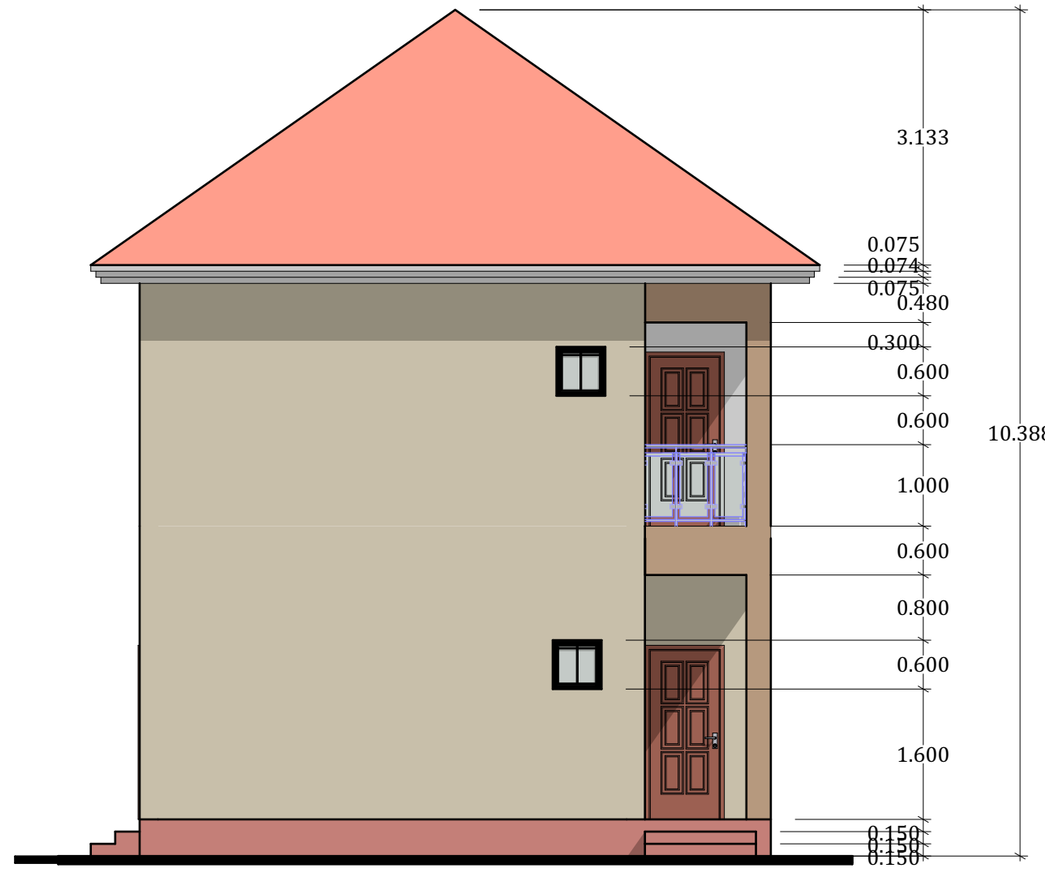

Project Title:

MULTIPURPOSE HALL AND 3 BEDROOM APARTMENT

bringing your vision to life...
Estrella Design

Designed by:	*Client:*	*Sheet Title:*	*Sheet Number:*
AKOROGIE PRECIOUS	MR ANDREW	**South and North Elevation**	4
Drawn by:	*Scale:*	*Date:*	
AKOROGIE PRECIOUS	1:100	August, 2025	






Project Title:

MULTIPURPOSE HALL AND 3 BEDROOM APARTMENT

bringing your vision to life...
Estrella Design

Designed by:	*Client:*	*Sheet Title:*	*Sheet Number:*
AKOROGIE PRECIOUS	MR ANDREW	**East and West Elevation**	5
Drawn by:	*Scale:*	*Date:*	
AKOROGIE PRECIOUS	1:100	August, 2025	

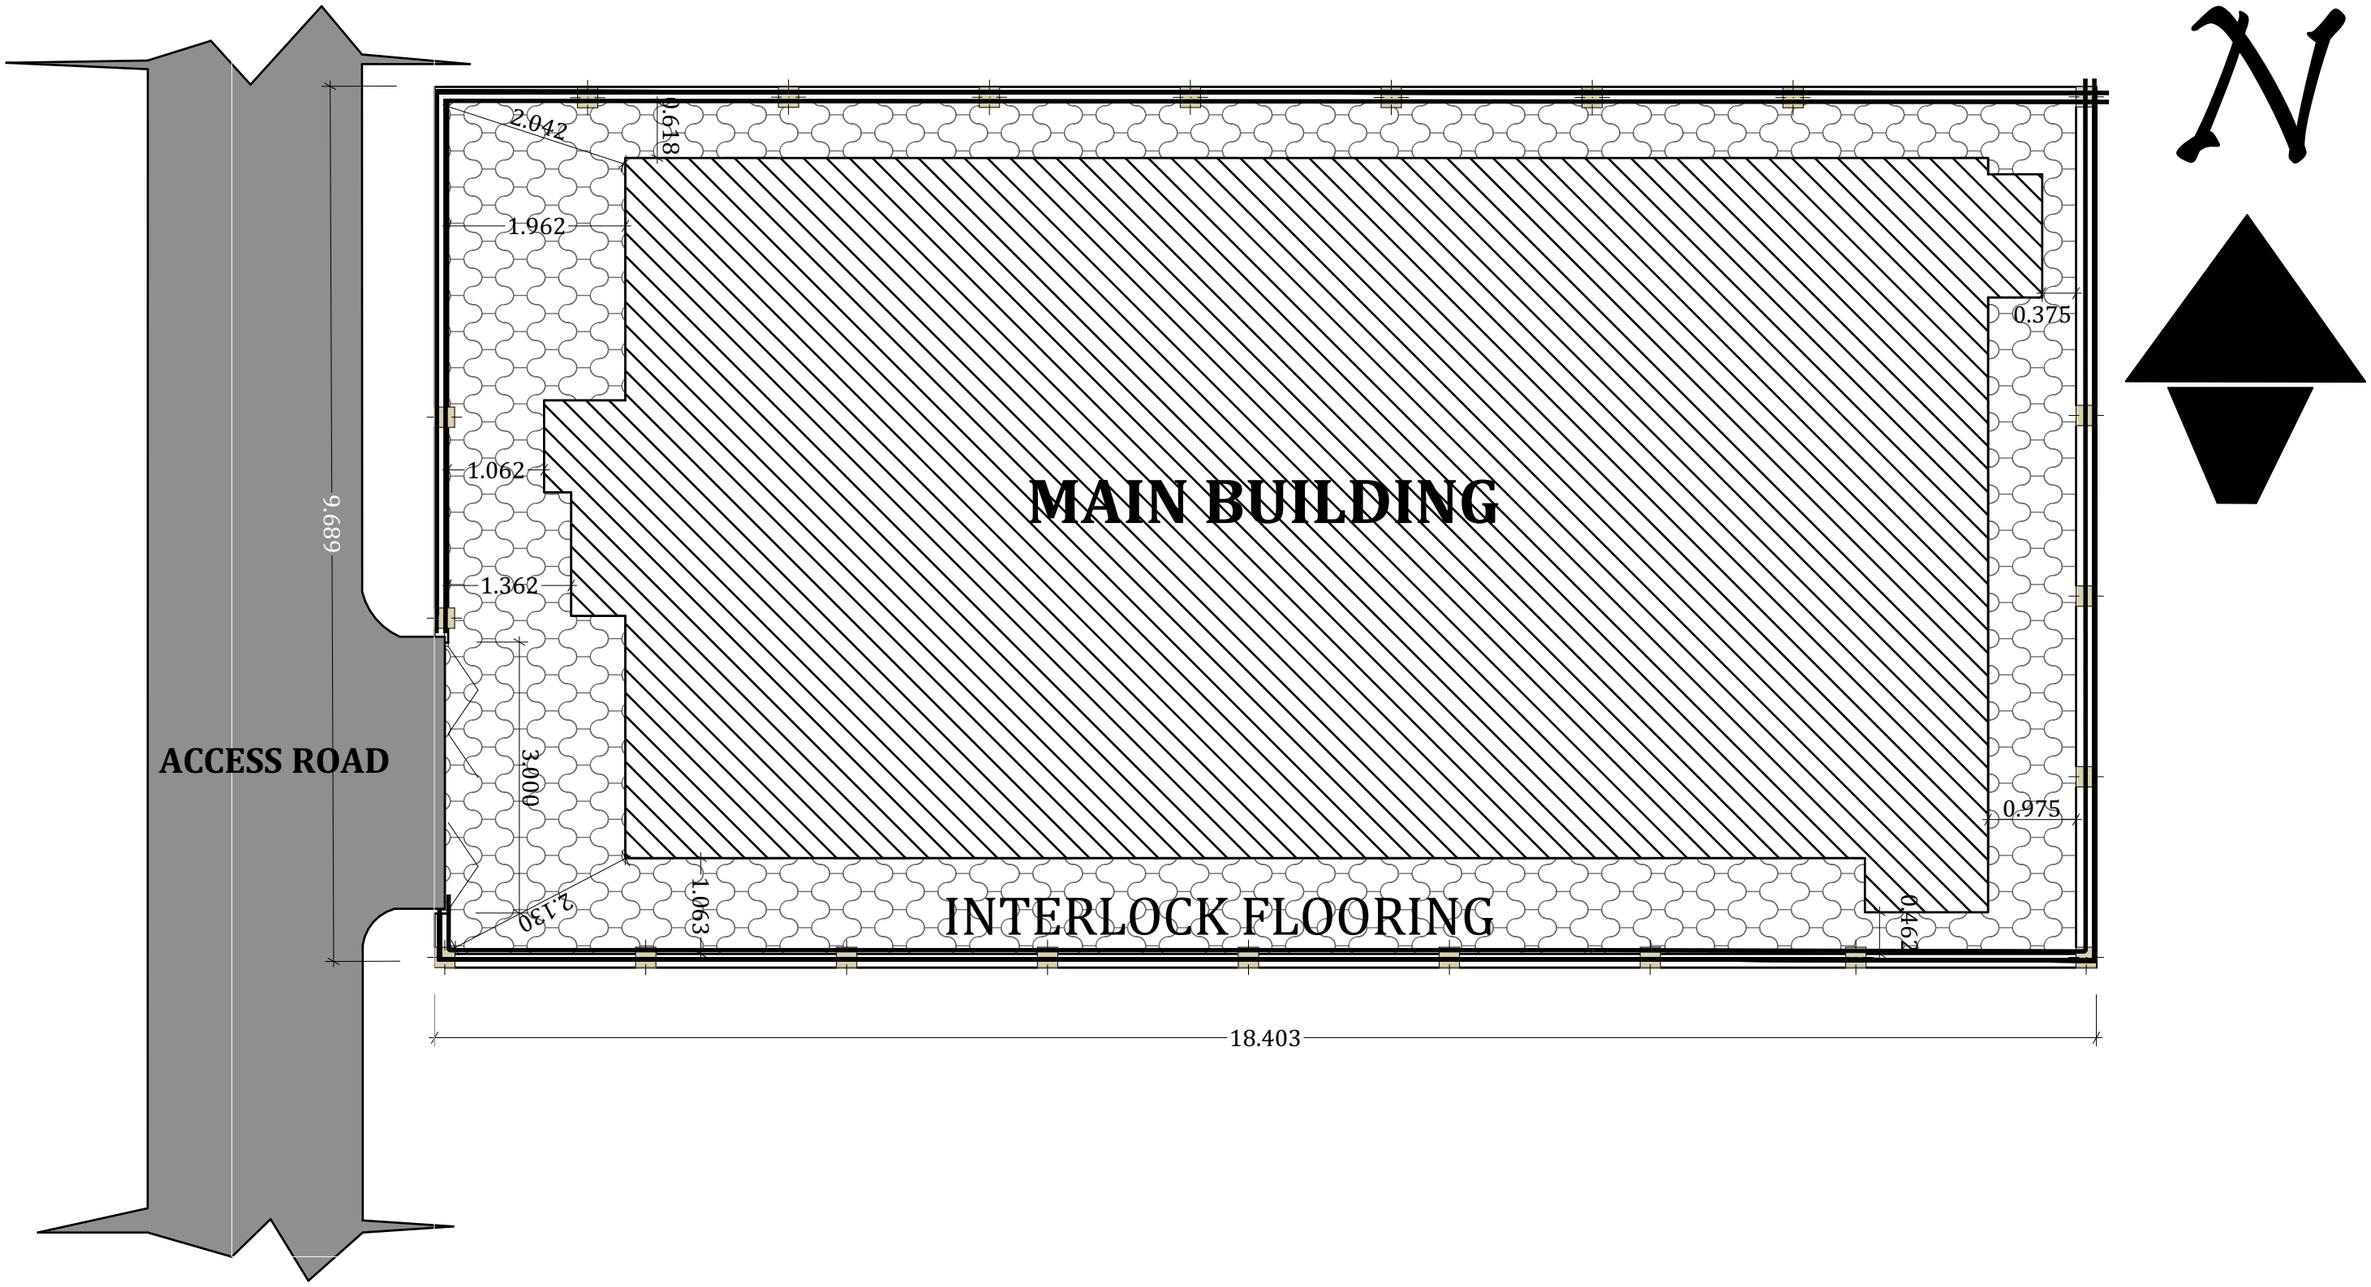

Project Title: **DINNING HALL AND THREE BEDROOM APARTMENT**		*Designed by:* AKOROGIE PRECIOUS	*Client:* MR ANDREW	*Sheet Title:* Site plan
		Drawn by: AKOROGIE PRECIOUS	*Scale:* 1:100	*Date:* August, 2025
	bringing your vision to life... Estrella Design			*Sheet Number:* 8





Project Title:

DINNING HALL AND THREE BEDROOM APARTMENT

bringing your vision to life...
Estrella Design

Designed by:	*Client:*	*Sheet Title:*	*Sheet Number:*
AKOROGIE PRECIOUS	MR ANDREW	3d views	9
Drawn by:	*Scale:*	*Date:*	
AKOROGIE PRECIOUS	1:100	August, 2025	